

FRAC.H



AREA NATURAL DE USO RECREATIVO, TURISTICO Y EDUCATIVO



JOSE INGENIEROS


FRAC.18

FRAC.17


Pc 2

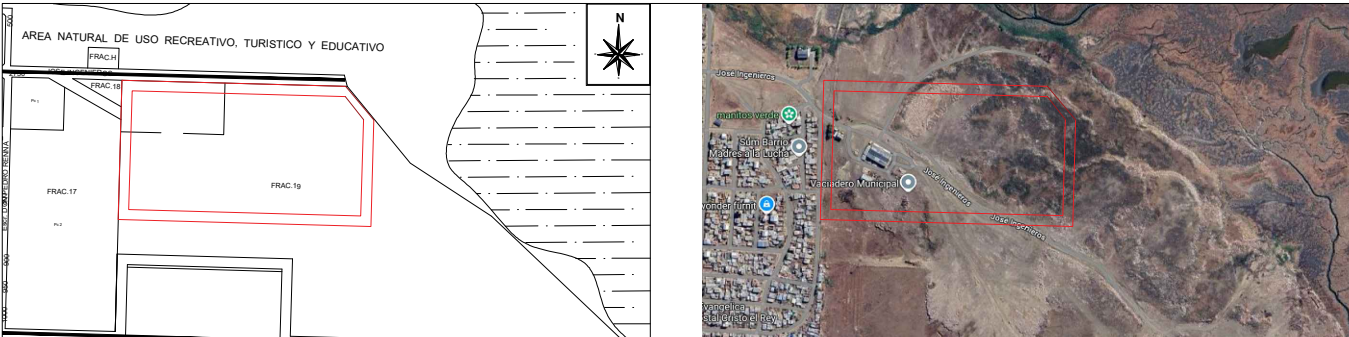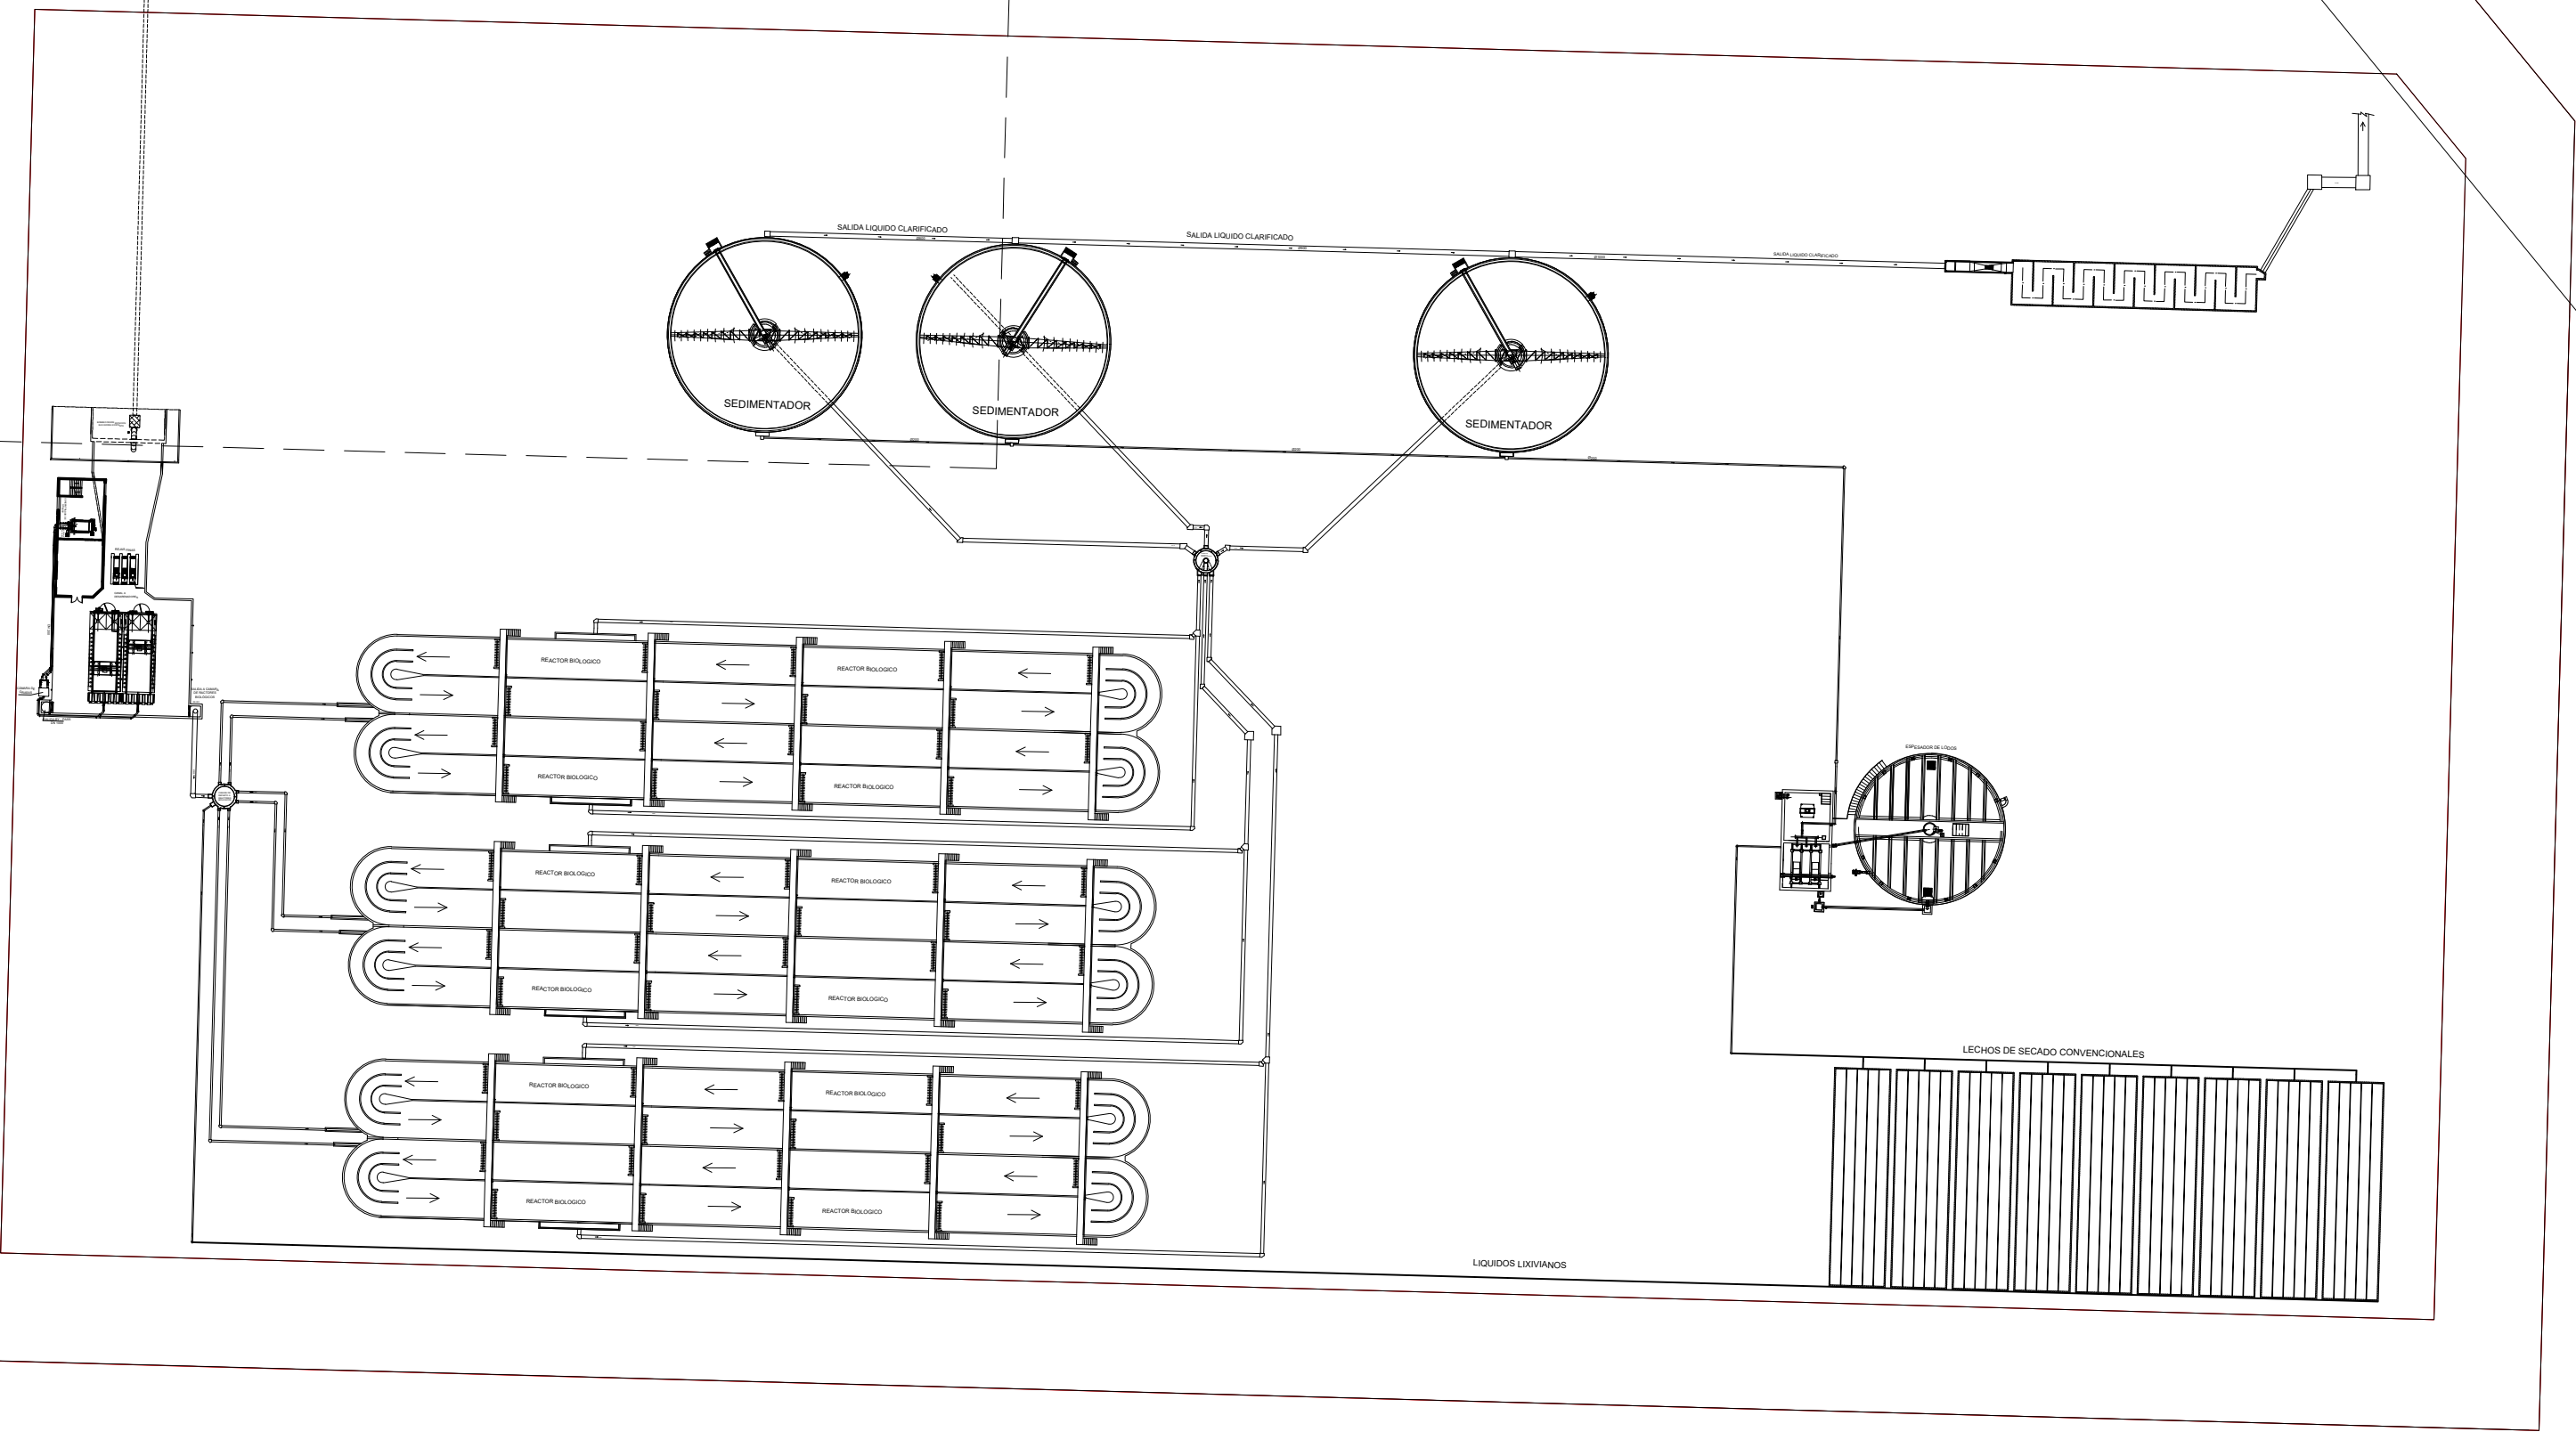


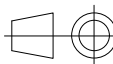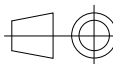	FECHA	NOMBRE	PROYECTO FINAL	 FACULTAD REGIONAL SANTA CRUZ UNIVERSIDAD TECNOLÓGICA NACIONAL
Dib.		Fernández, Juan I.		
Rev.				
Apr.				
ESCALA: 1/1000				Visado
				Plano: UBICACIÓN GENERAL
				Código: PL - 001

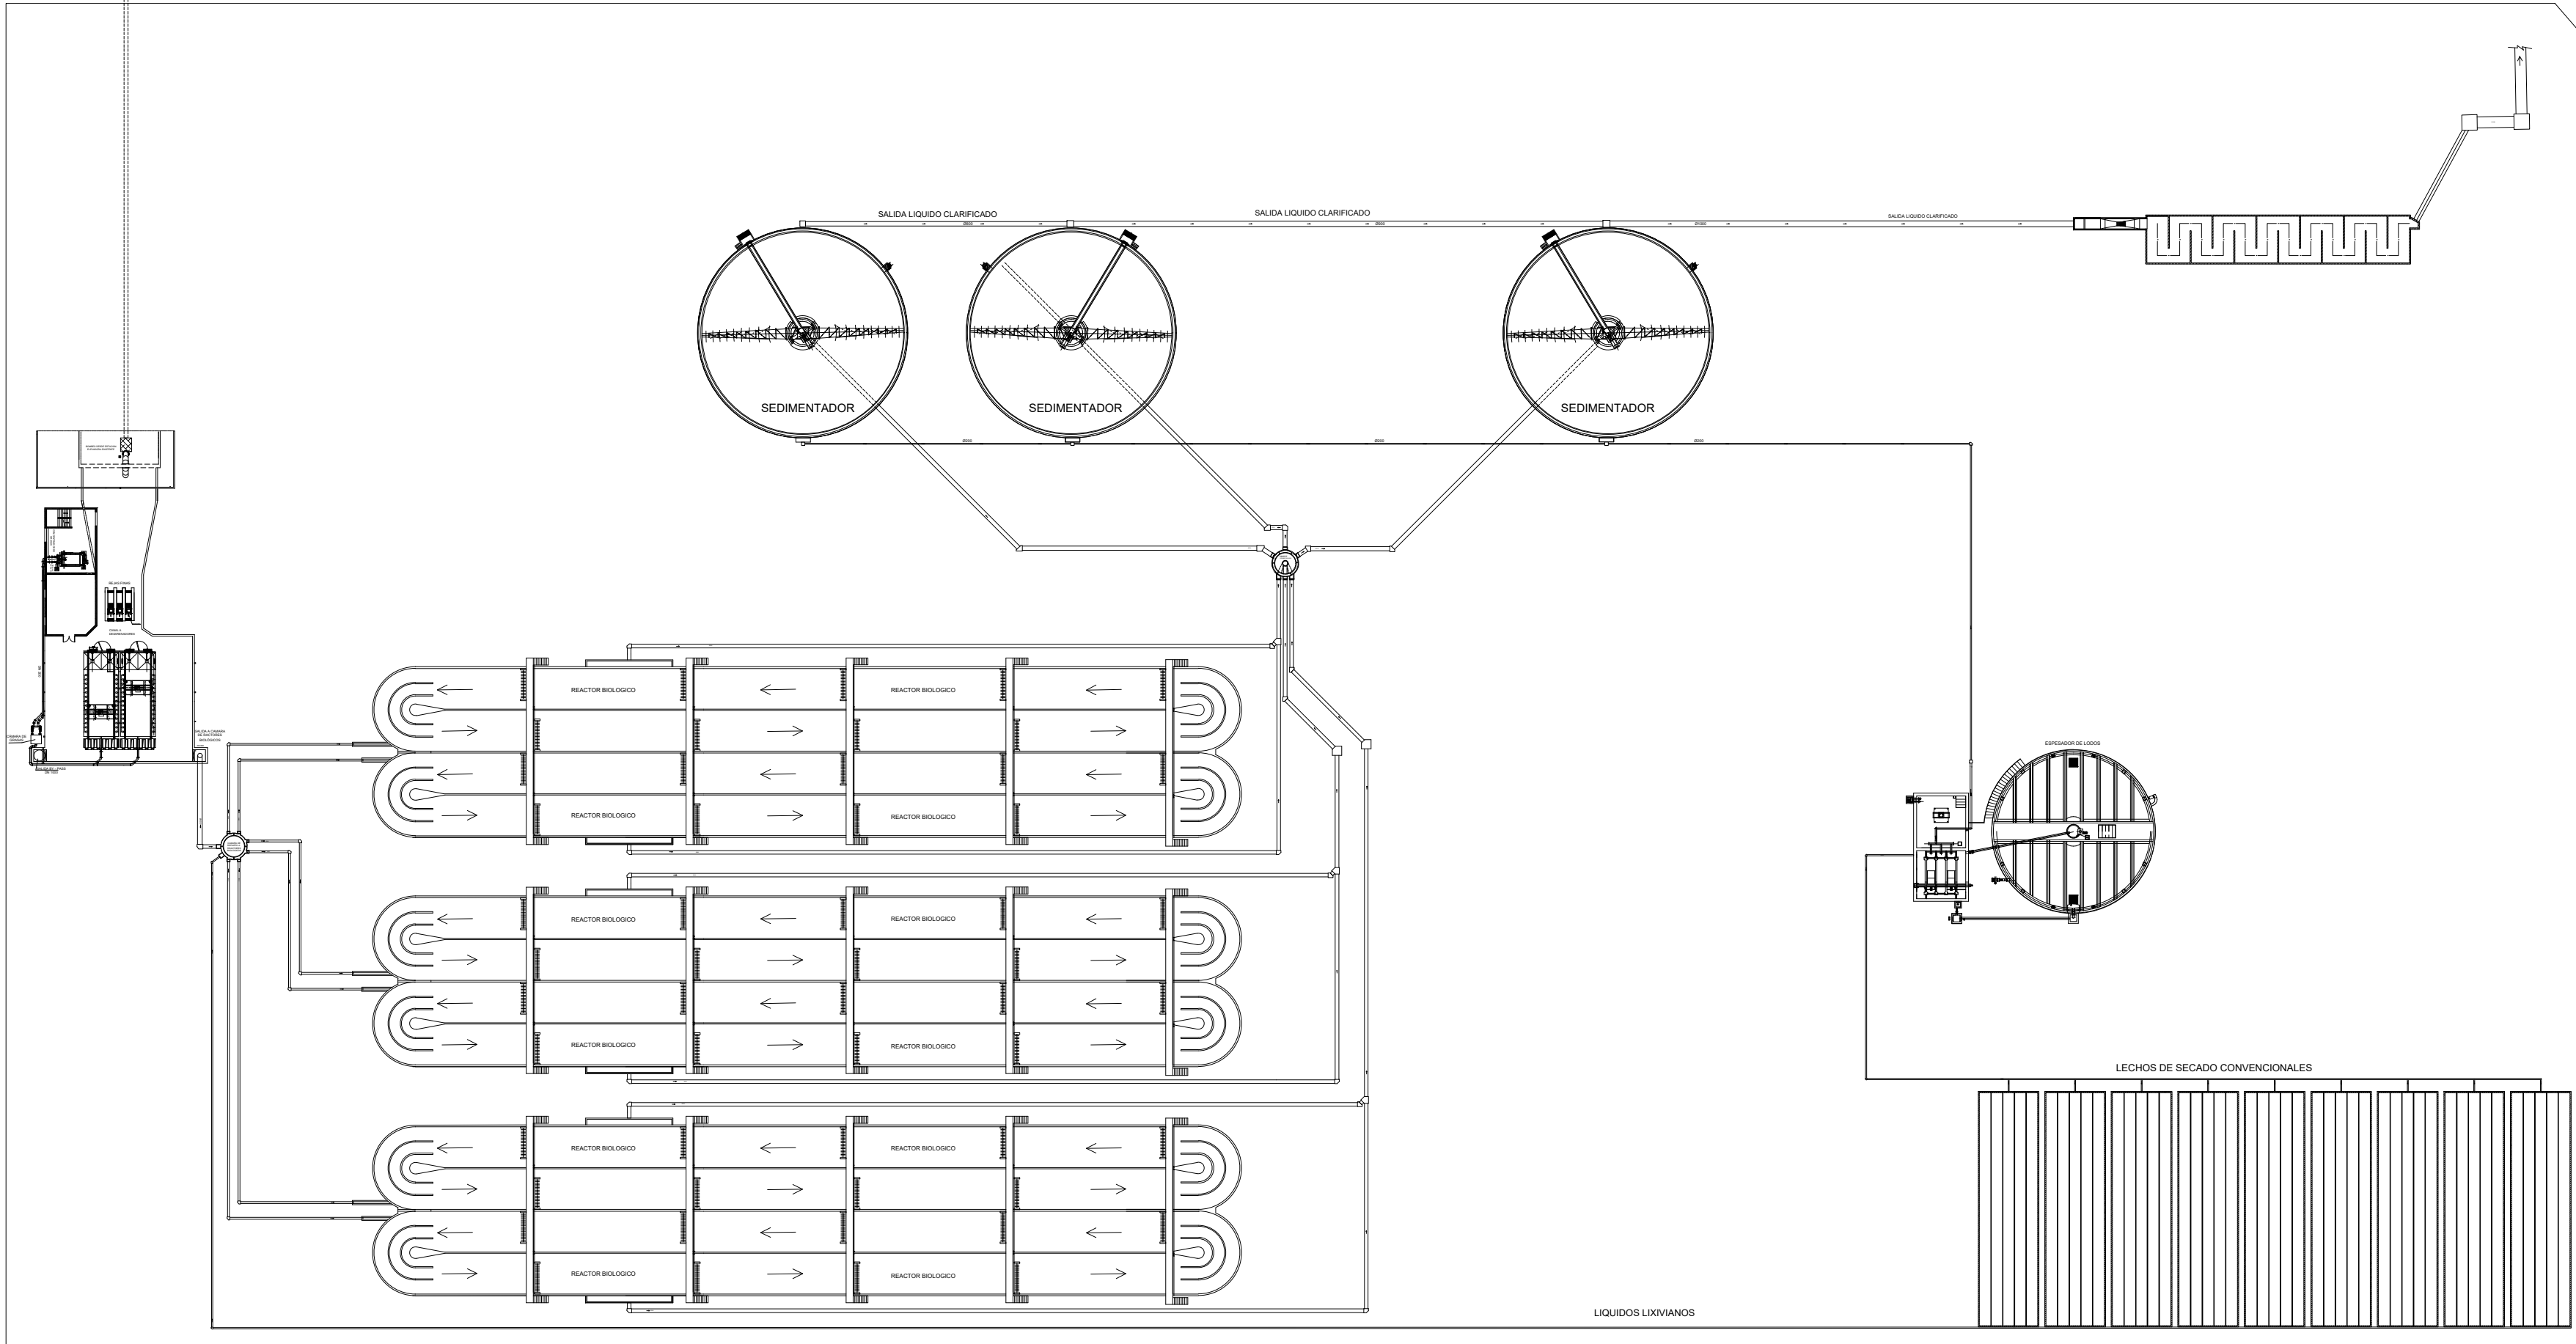


		FECHA	NOMBRE	PROYECTO FINAL	 FACULTAD REGIONAL SANTA CRUZ UNIVERSIDAD TECNOLÓGICA NACIONAL
Dib.			Fernández, Juan I.		
Rev.					
Apr.					
ESCALA: 1/950					Visado
					
Toler. Rug.					
					Plano: LAYOUT
					Código: PL - 002

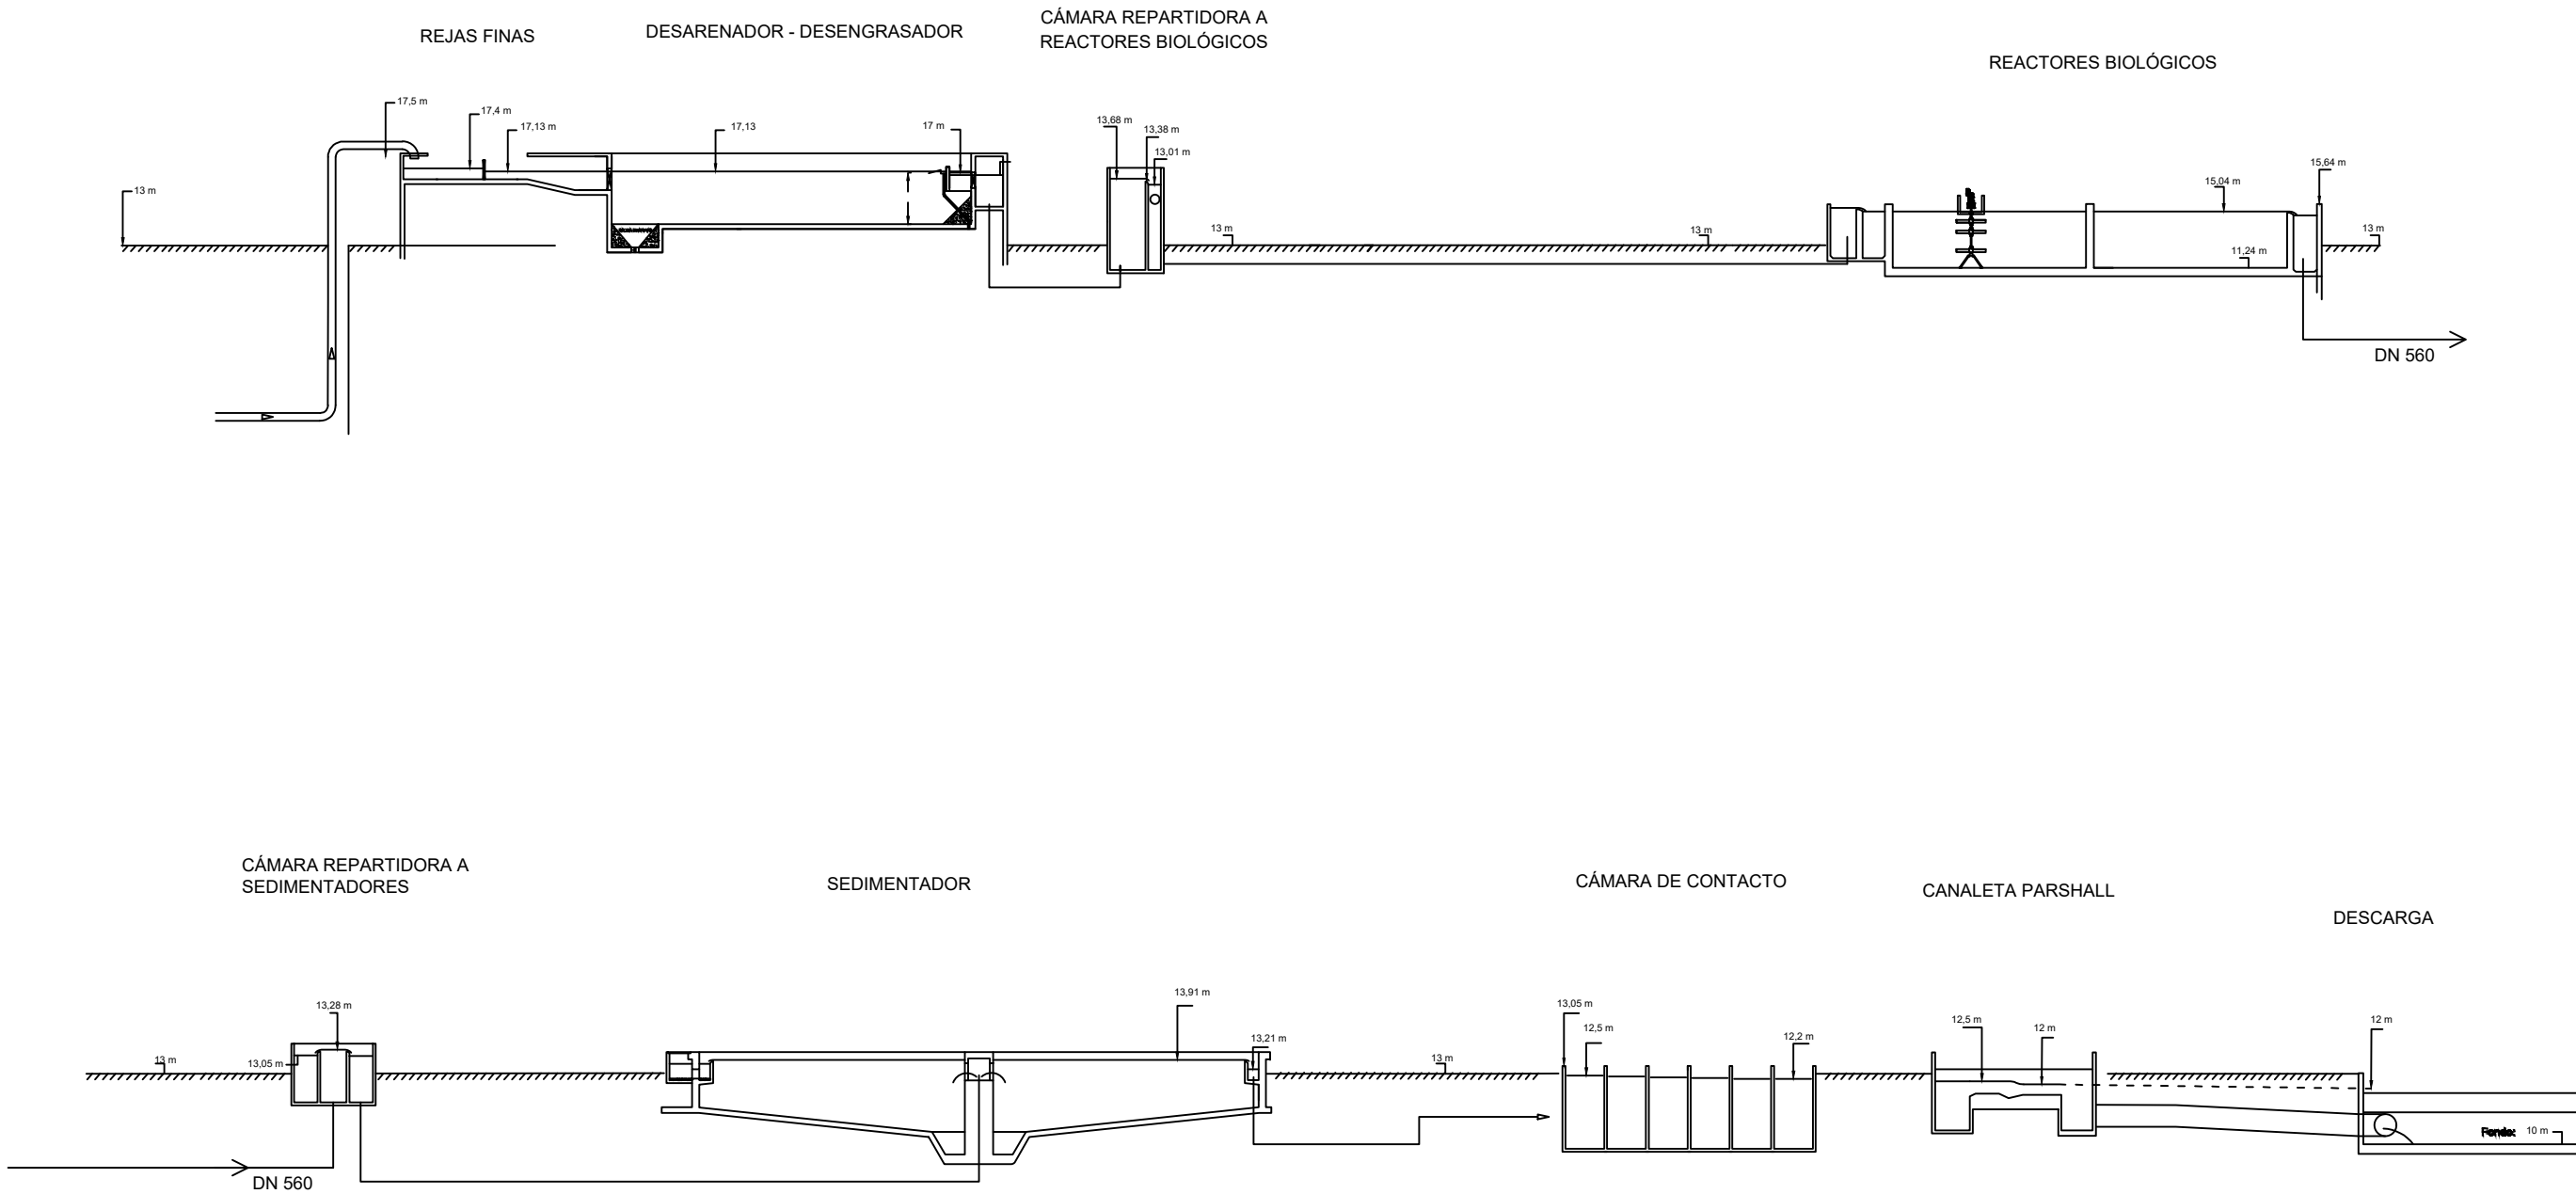


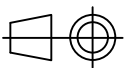		FECHA	NOMBRE	PROYECTO FINAL	 FACULTAD REGIONAL SANTA CRUZ UNIVERSIDAD TECNOLÓGICA NACIONAL
	Dib.		Fernández, Juan I.		
	Rev.				
	Apr.				
ESCALA: S/E					Visado
					
Toler. Rug.					
					Plano: PERFIL HIDRÁULICO
					Código: PL - 003



PLANTA

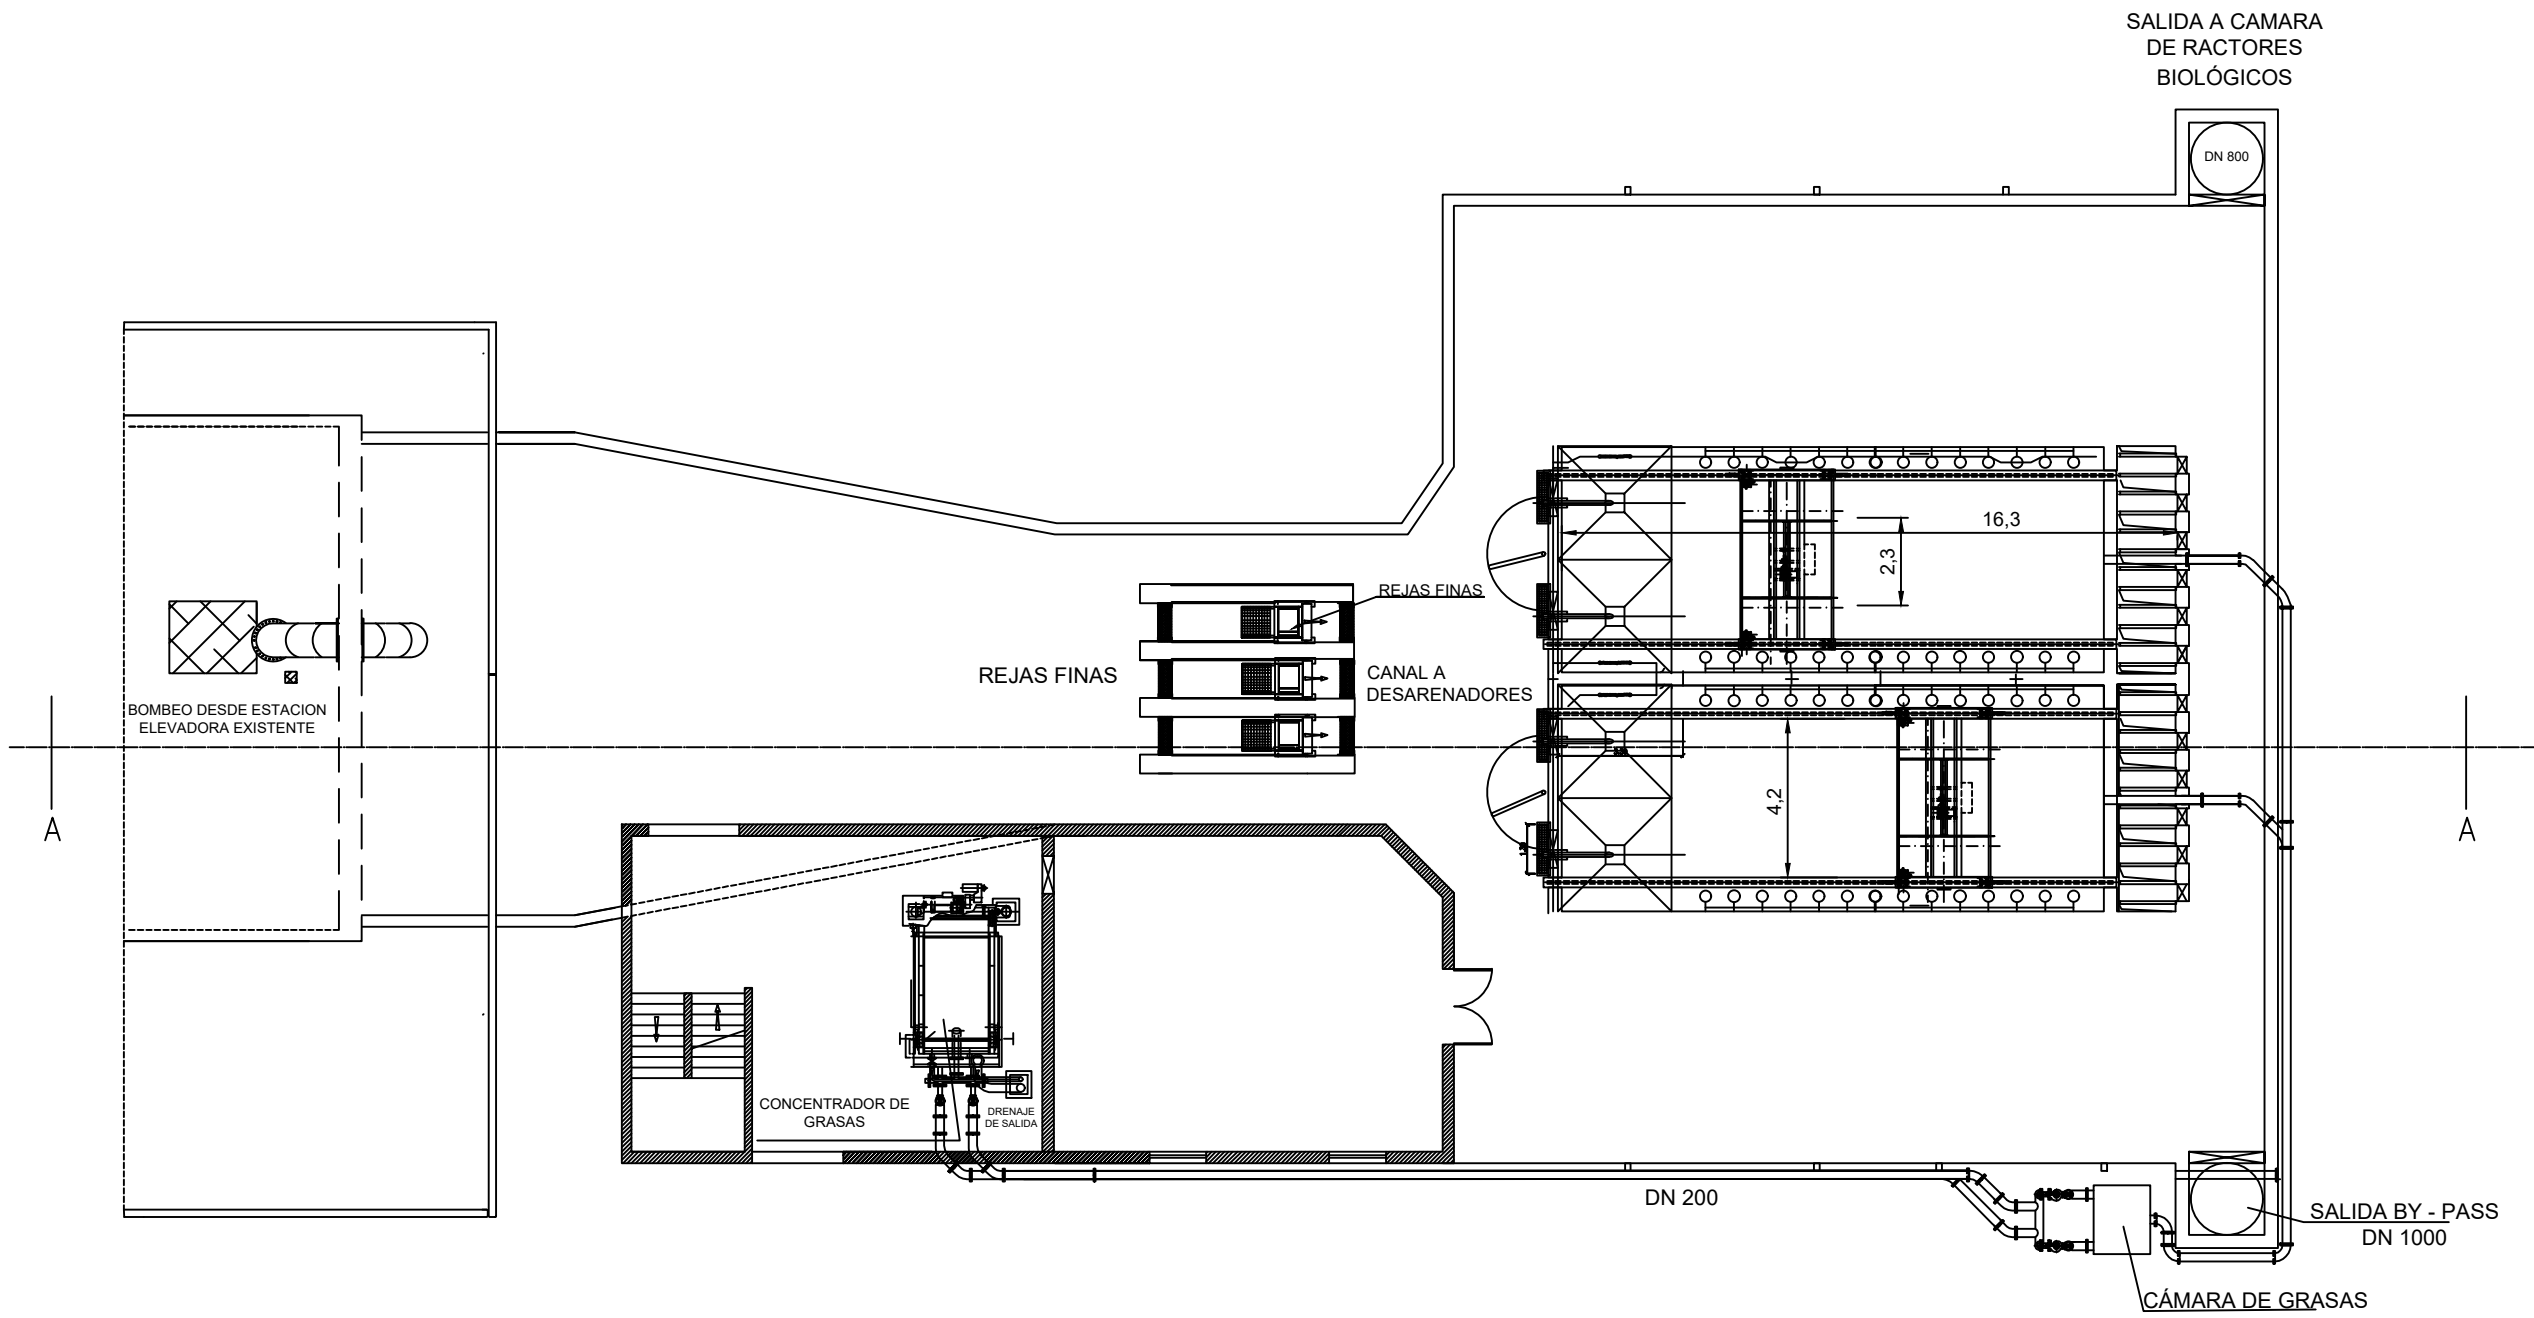


CORTE A - A

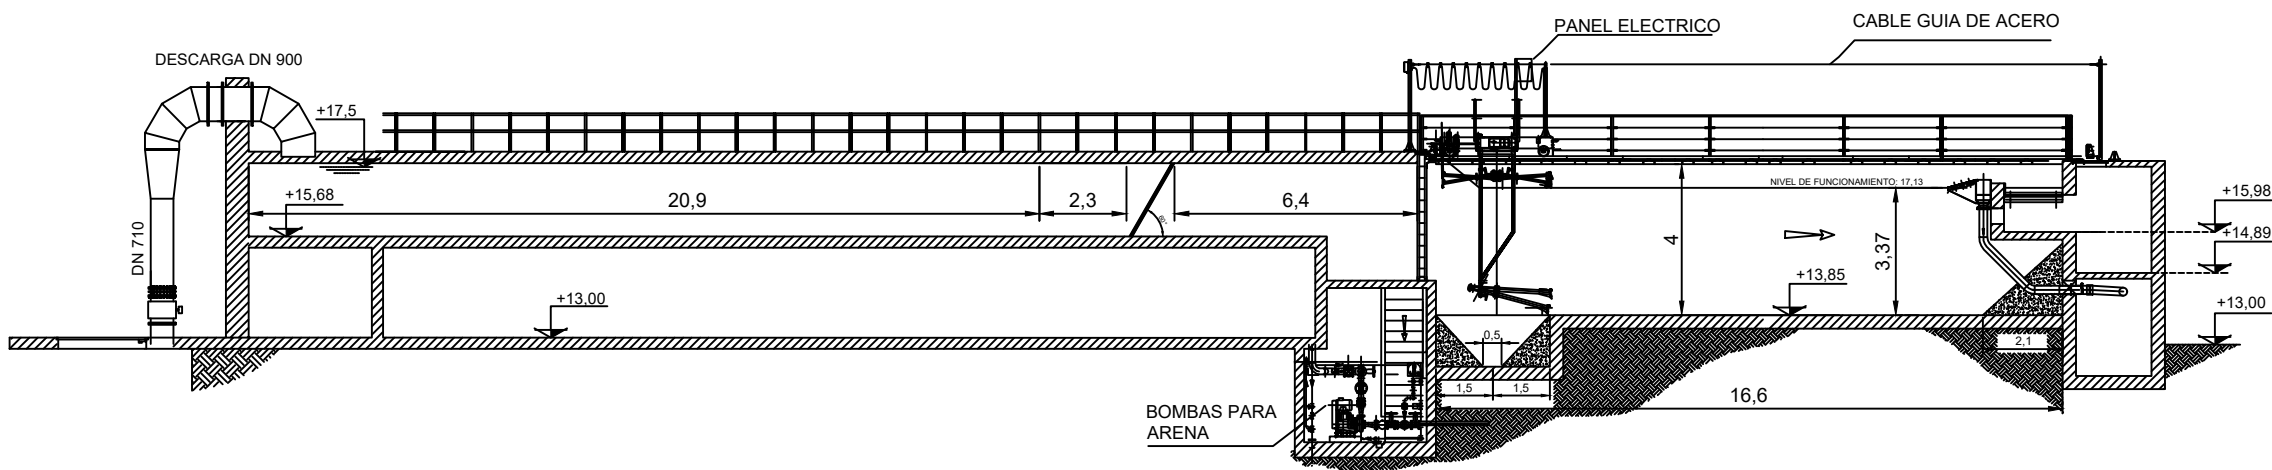


		FECHA	NOMBRE	PROYECTO FINAL	FACULTAD REGIONAL SANTA CRUZ UNIVERSIDAD TECNOLÓGICA NACIONAL
Dib.		Fernández, Juan I.			
Rev.					
Apr.					
ESCALA: 1:200					Visado
					
Toler. Rug.					
					Plano: UNIDAD DE PRETRATAMIENTO - REJAS FINAS Y DESARENADOR
					Código: PL - 004

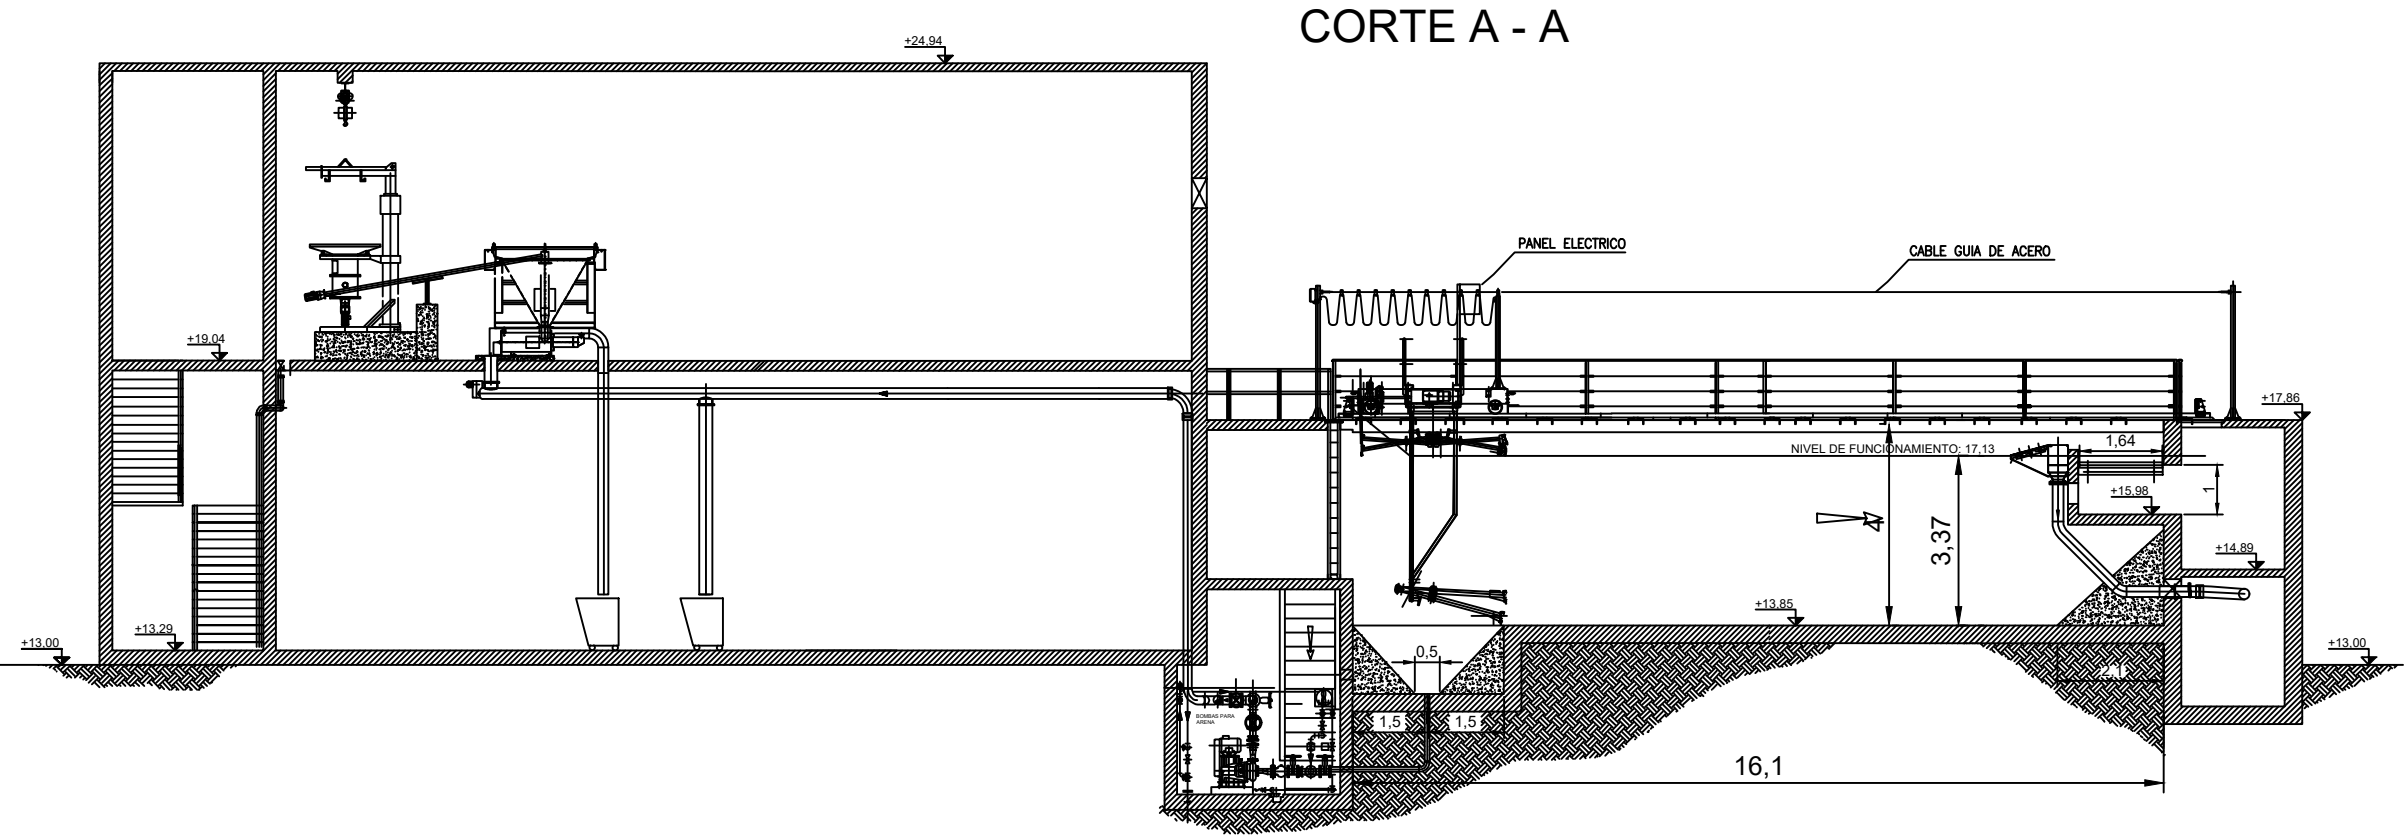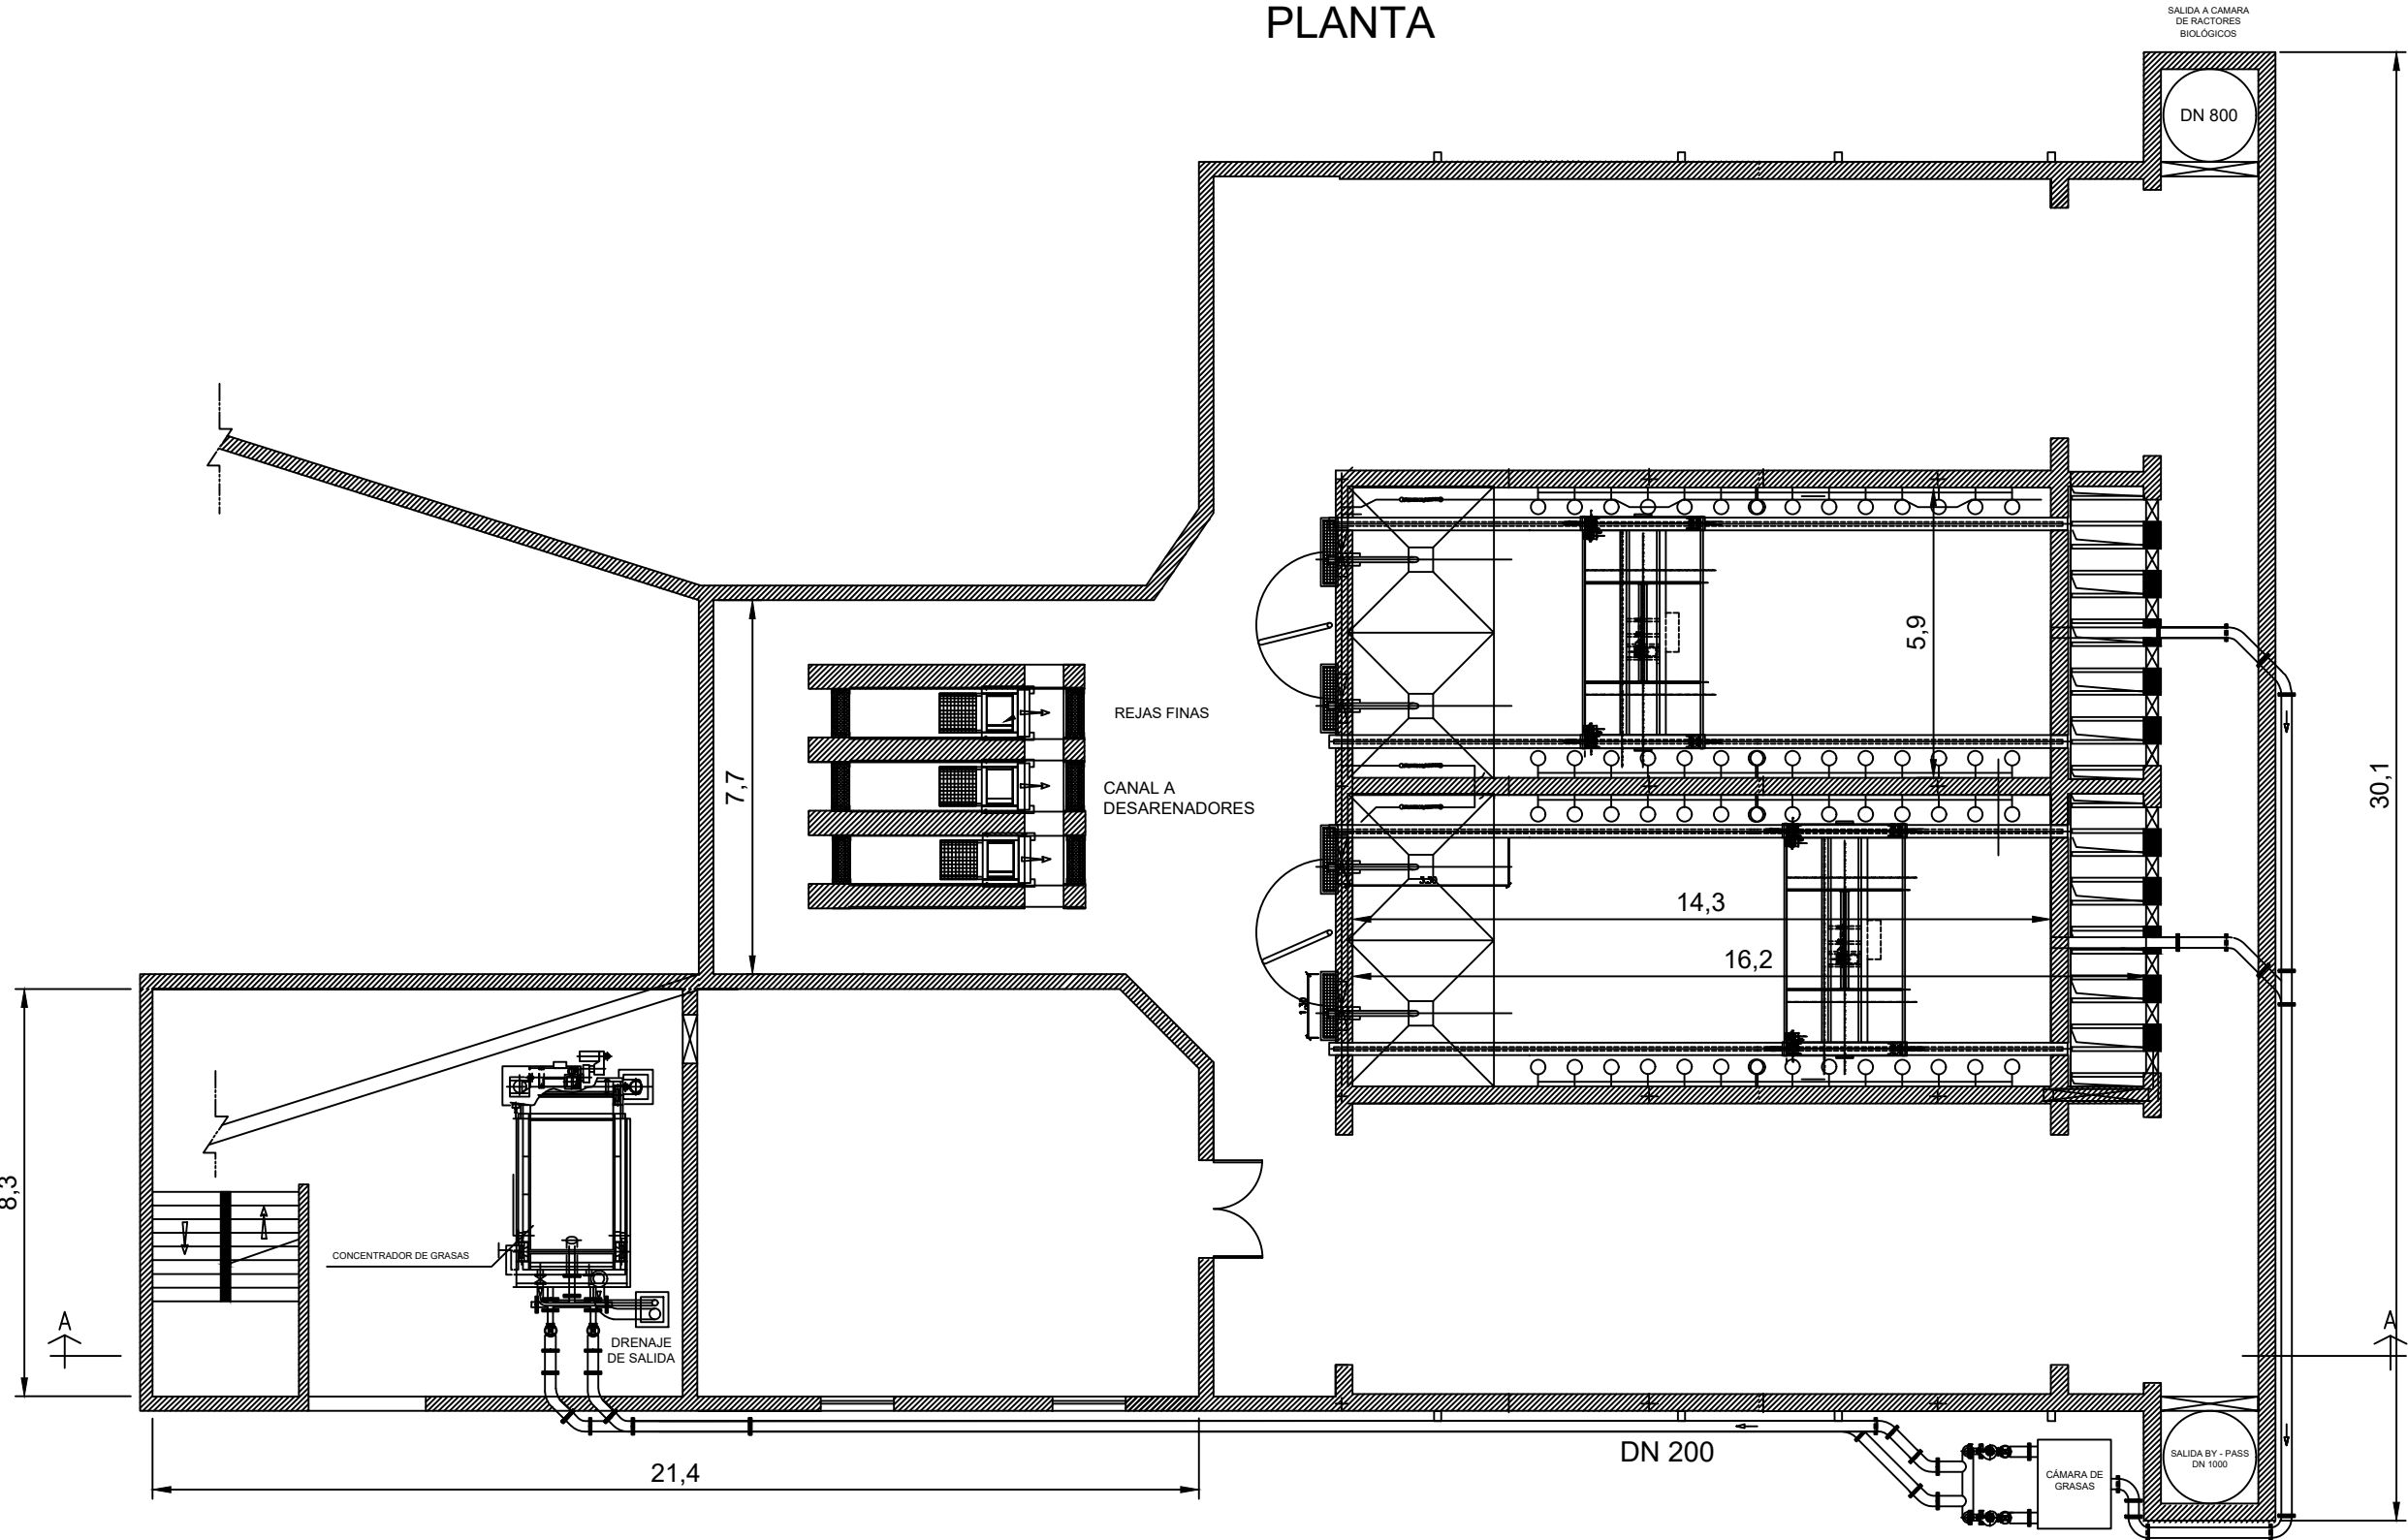



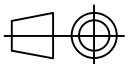
	FECHA	NOMBRE	PROYECTO FINAL	 FACULTAD REGIONAL SANTA CRUZ UNIVERSIDAD TECNOLÓGICA NACIONAL
Dib.		Fernández, Juan I.		
Rev.				
Apr.				
ESCALA: 1:150				Visado
				Plano: DESARENADOR - PLANTA - CORTES
Toler. Rug.				Código: PL - 005




CÁMARA DE REPARTO A REACTORES BIOLÓGICOS

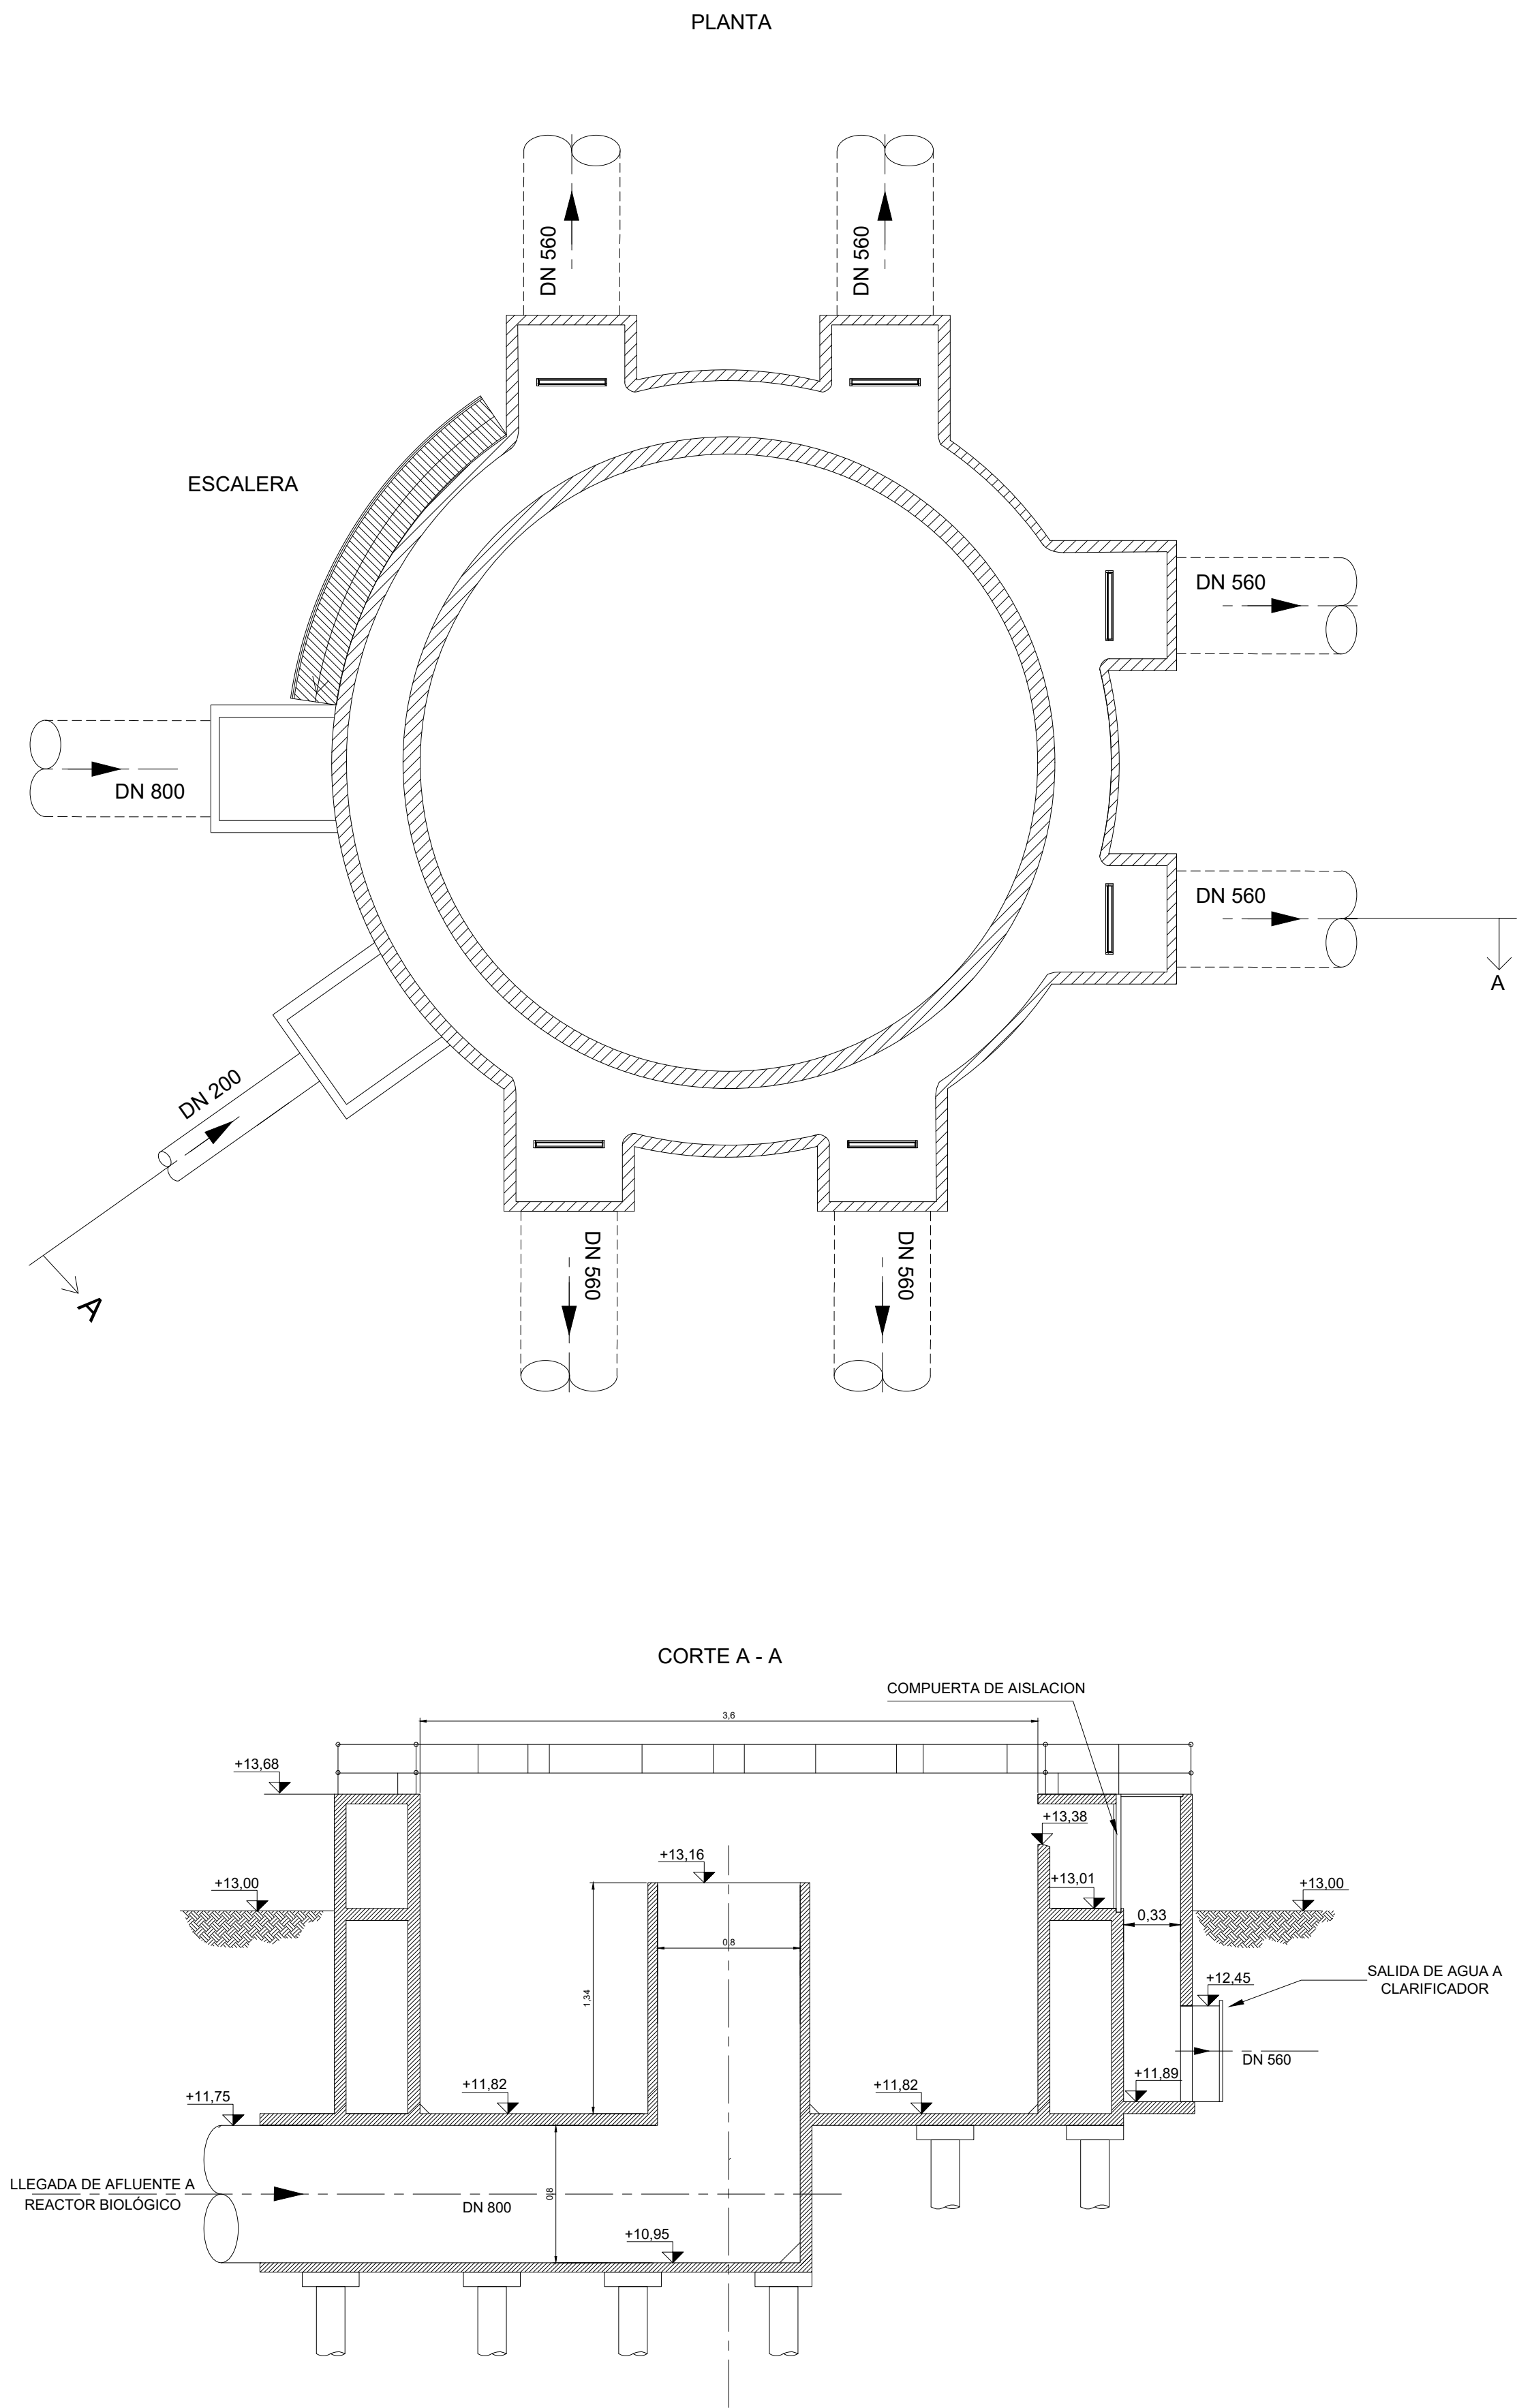


CÁMARA DE REPARTO A SEDIMENTADORES

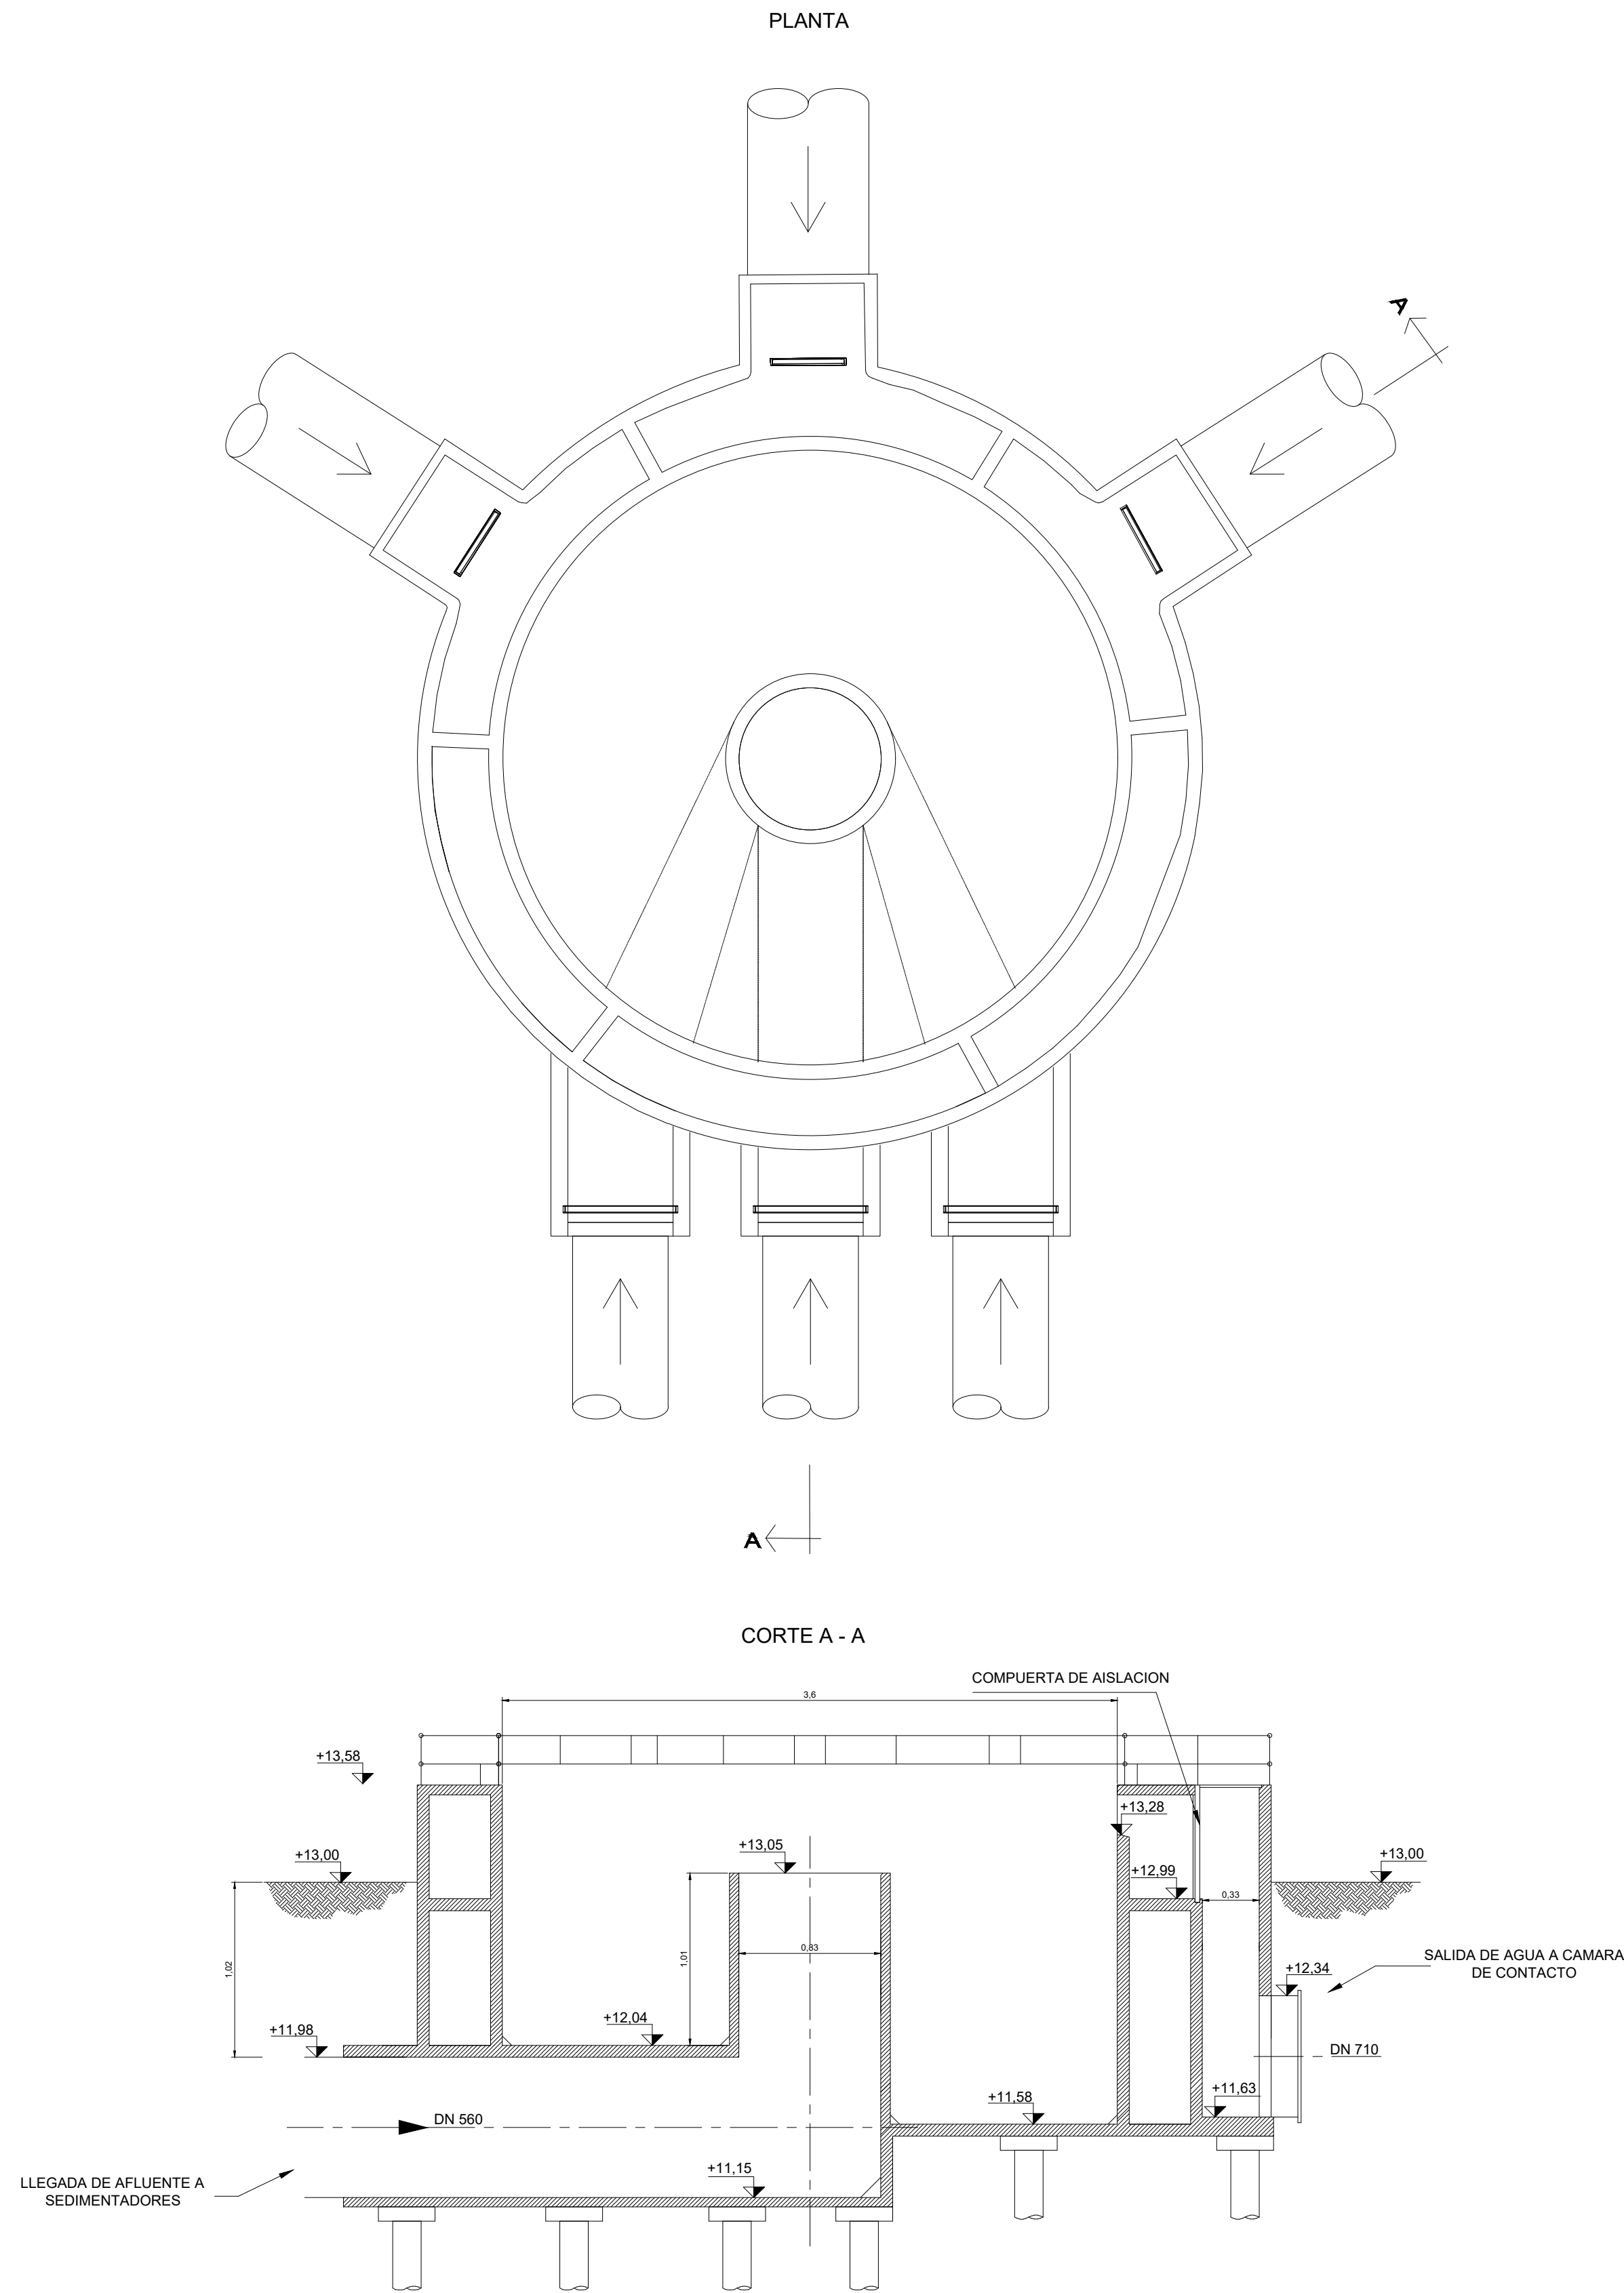


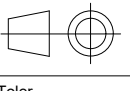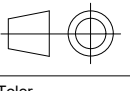FECHA		NOMBRE	PROYECTO FINAL	 UTN FACULTAD REGIONAL SACATEPEQUE UNIVERSIDAD TECNOLÓGICA NACIONAL
Dib.		Fernández, Juan I.		
Rev.				
Apr.				
ESCALA: 1:30				Visado
				
Taller: Ráp				
			Plano: CÁMARA DE DISTRIBUCIÓN	
			Código: PL - 006	

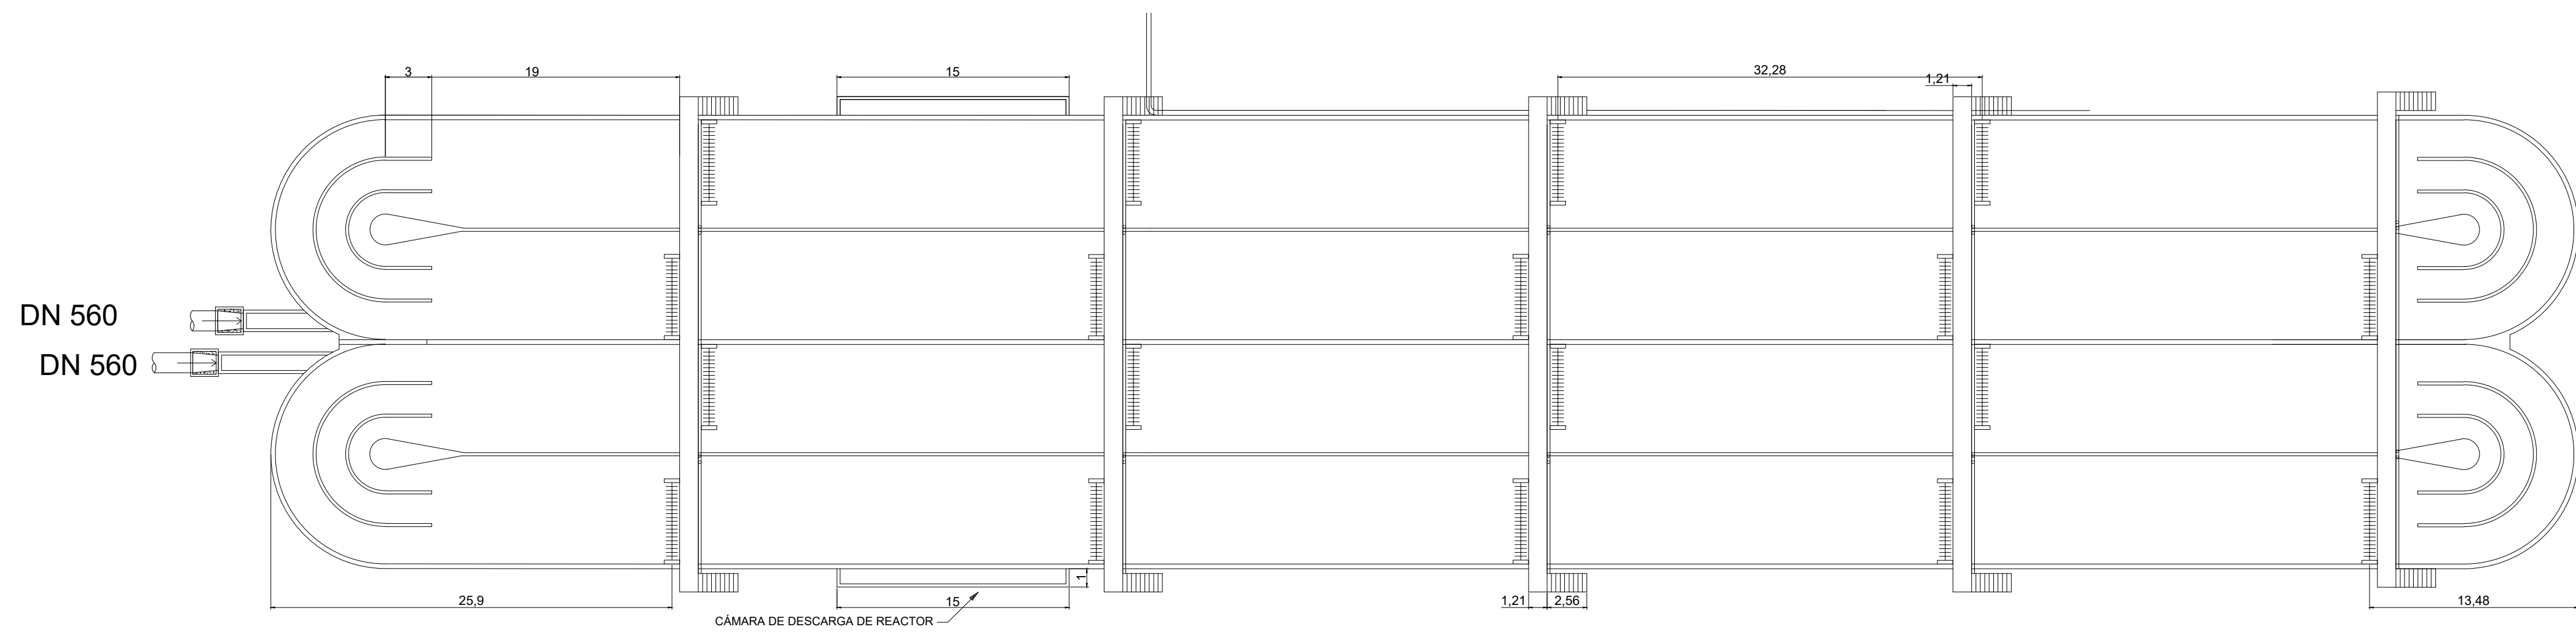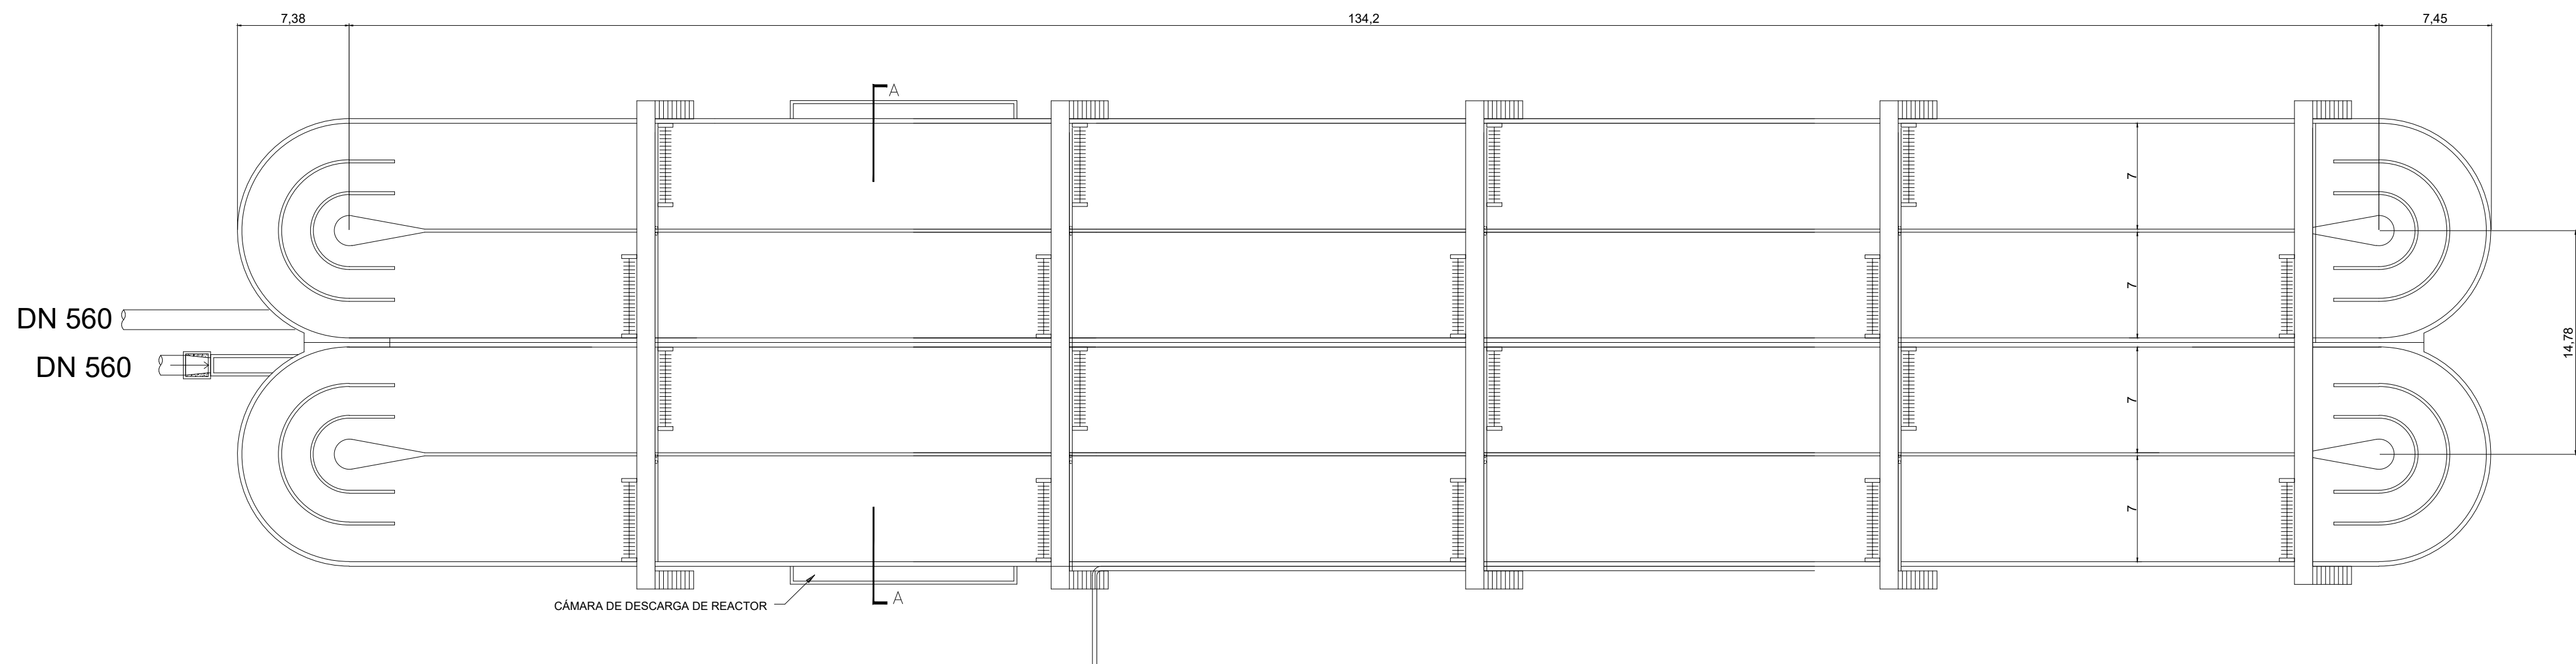
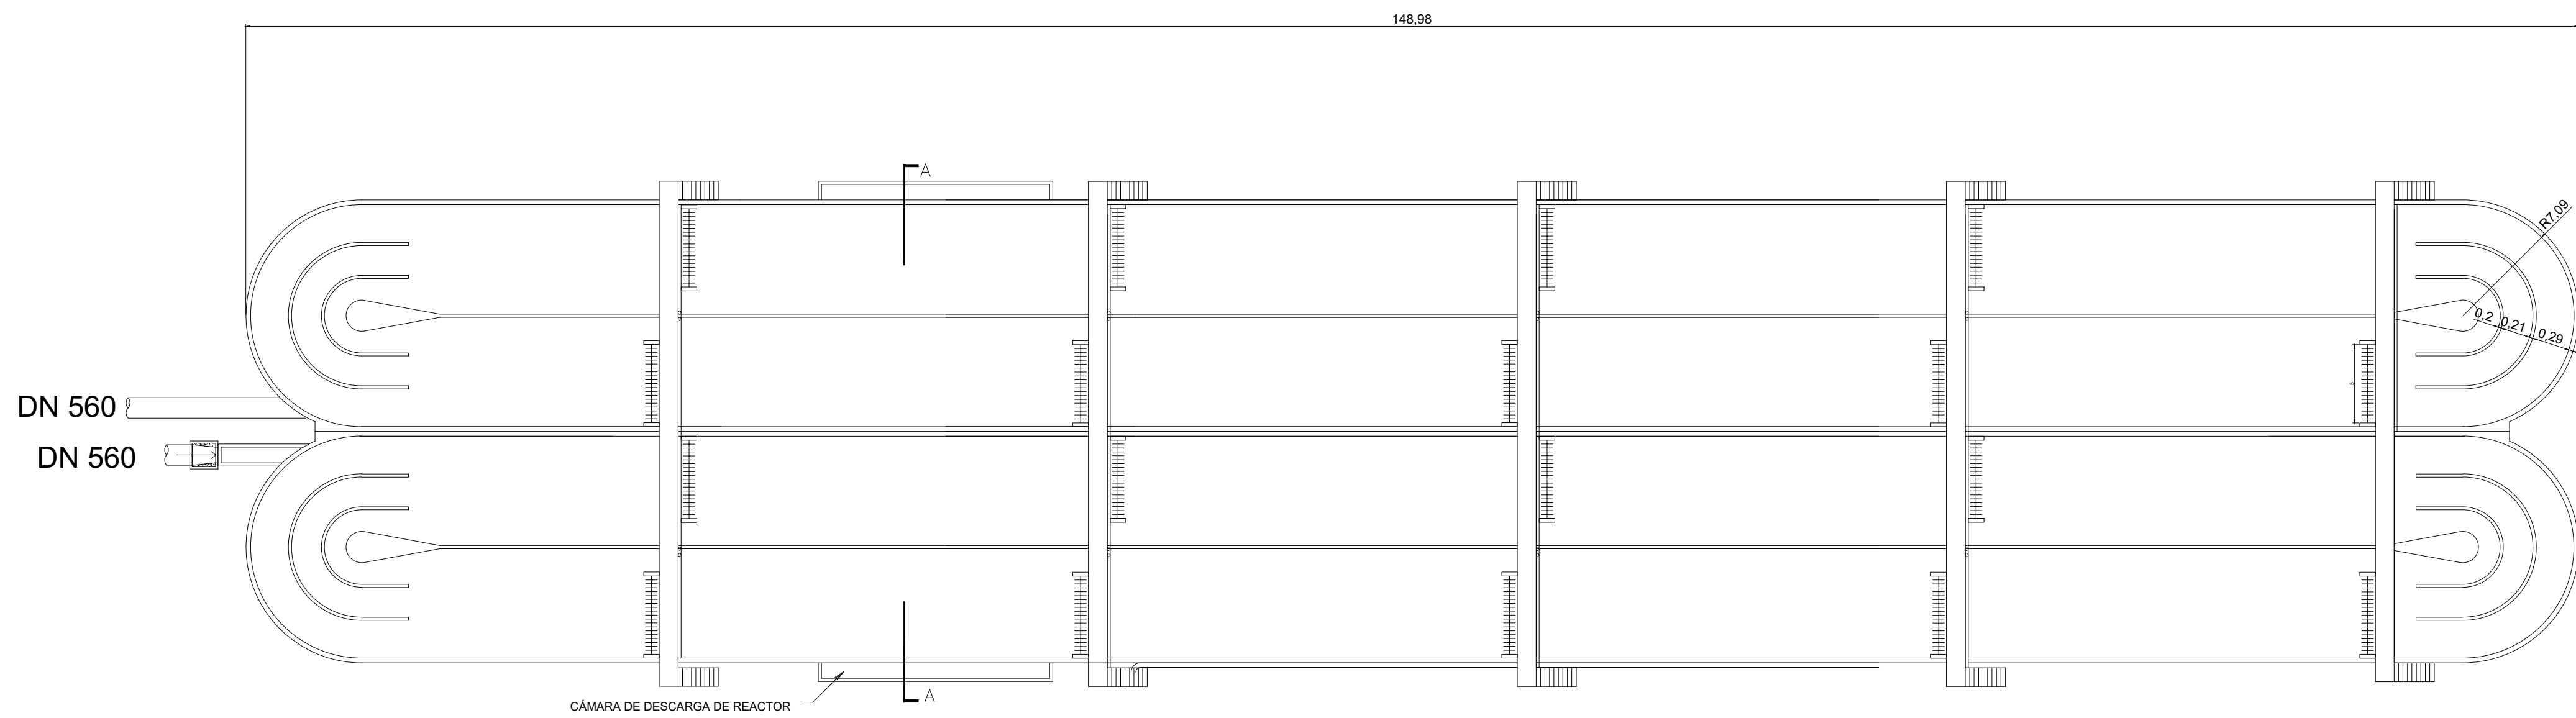


 
		FECHA	NOMBRE	PROYECTO FINAL	 UTN UNIVERSIDAD TECNOLÓGICA NACIONAL FACULTAD REGIONAL MACHOQUE
	Dib.		Fernández, Juan I.		
	Rev.				
	Apr.				
	ESCALA: 1/300				Vistado
					
	Toler. Rug.				
					Plano: REACTOR BIOLÓGICO - PLANTA
					Código: PL - 007




CORTE A - A
ESCALA: 1:50

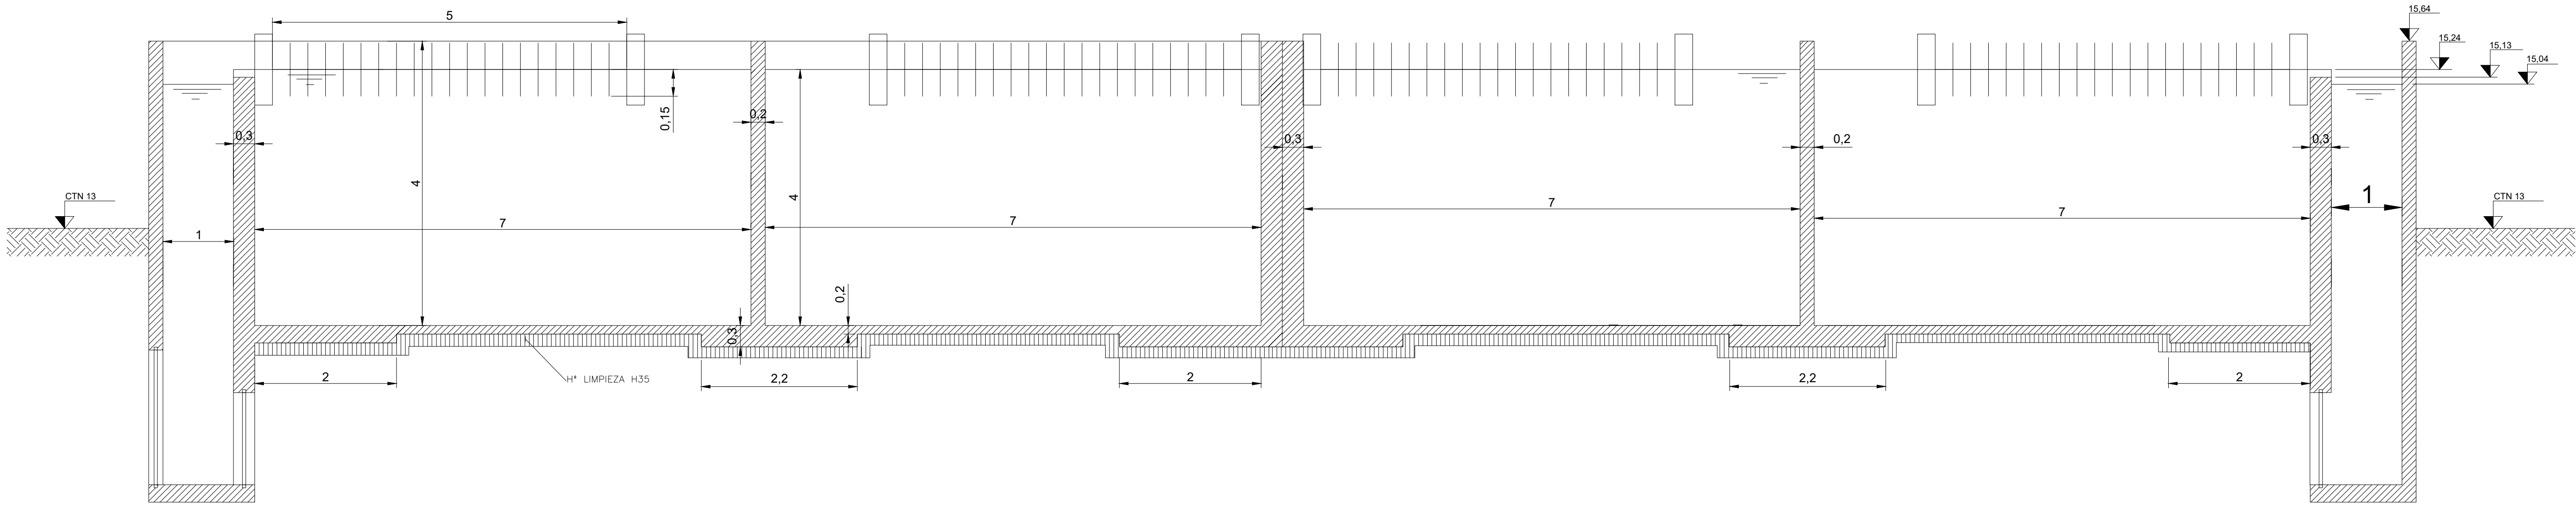


DETALLE PLANTA
ESCALA: 1:75

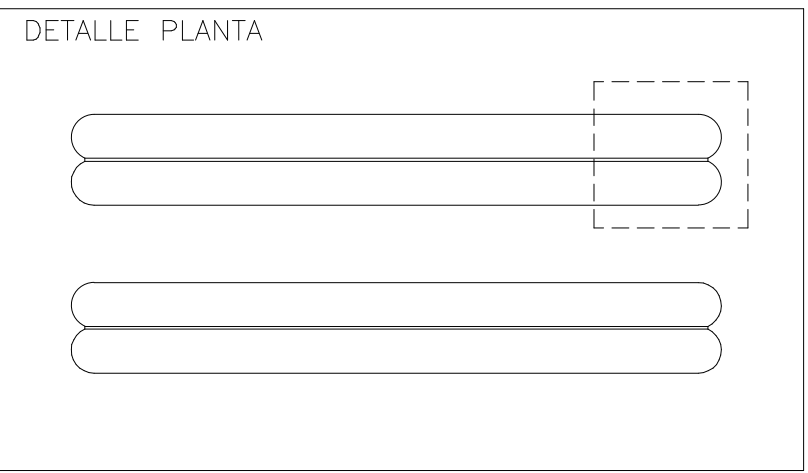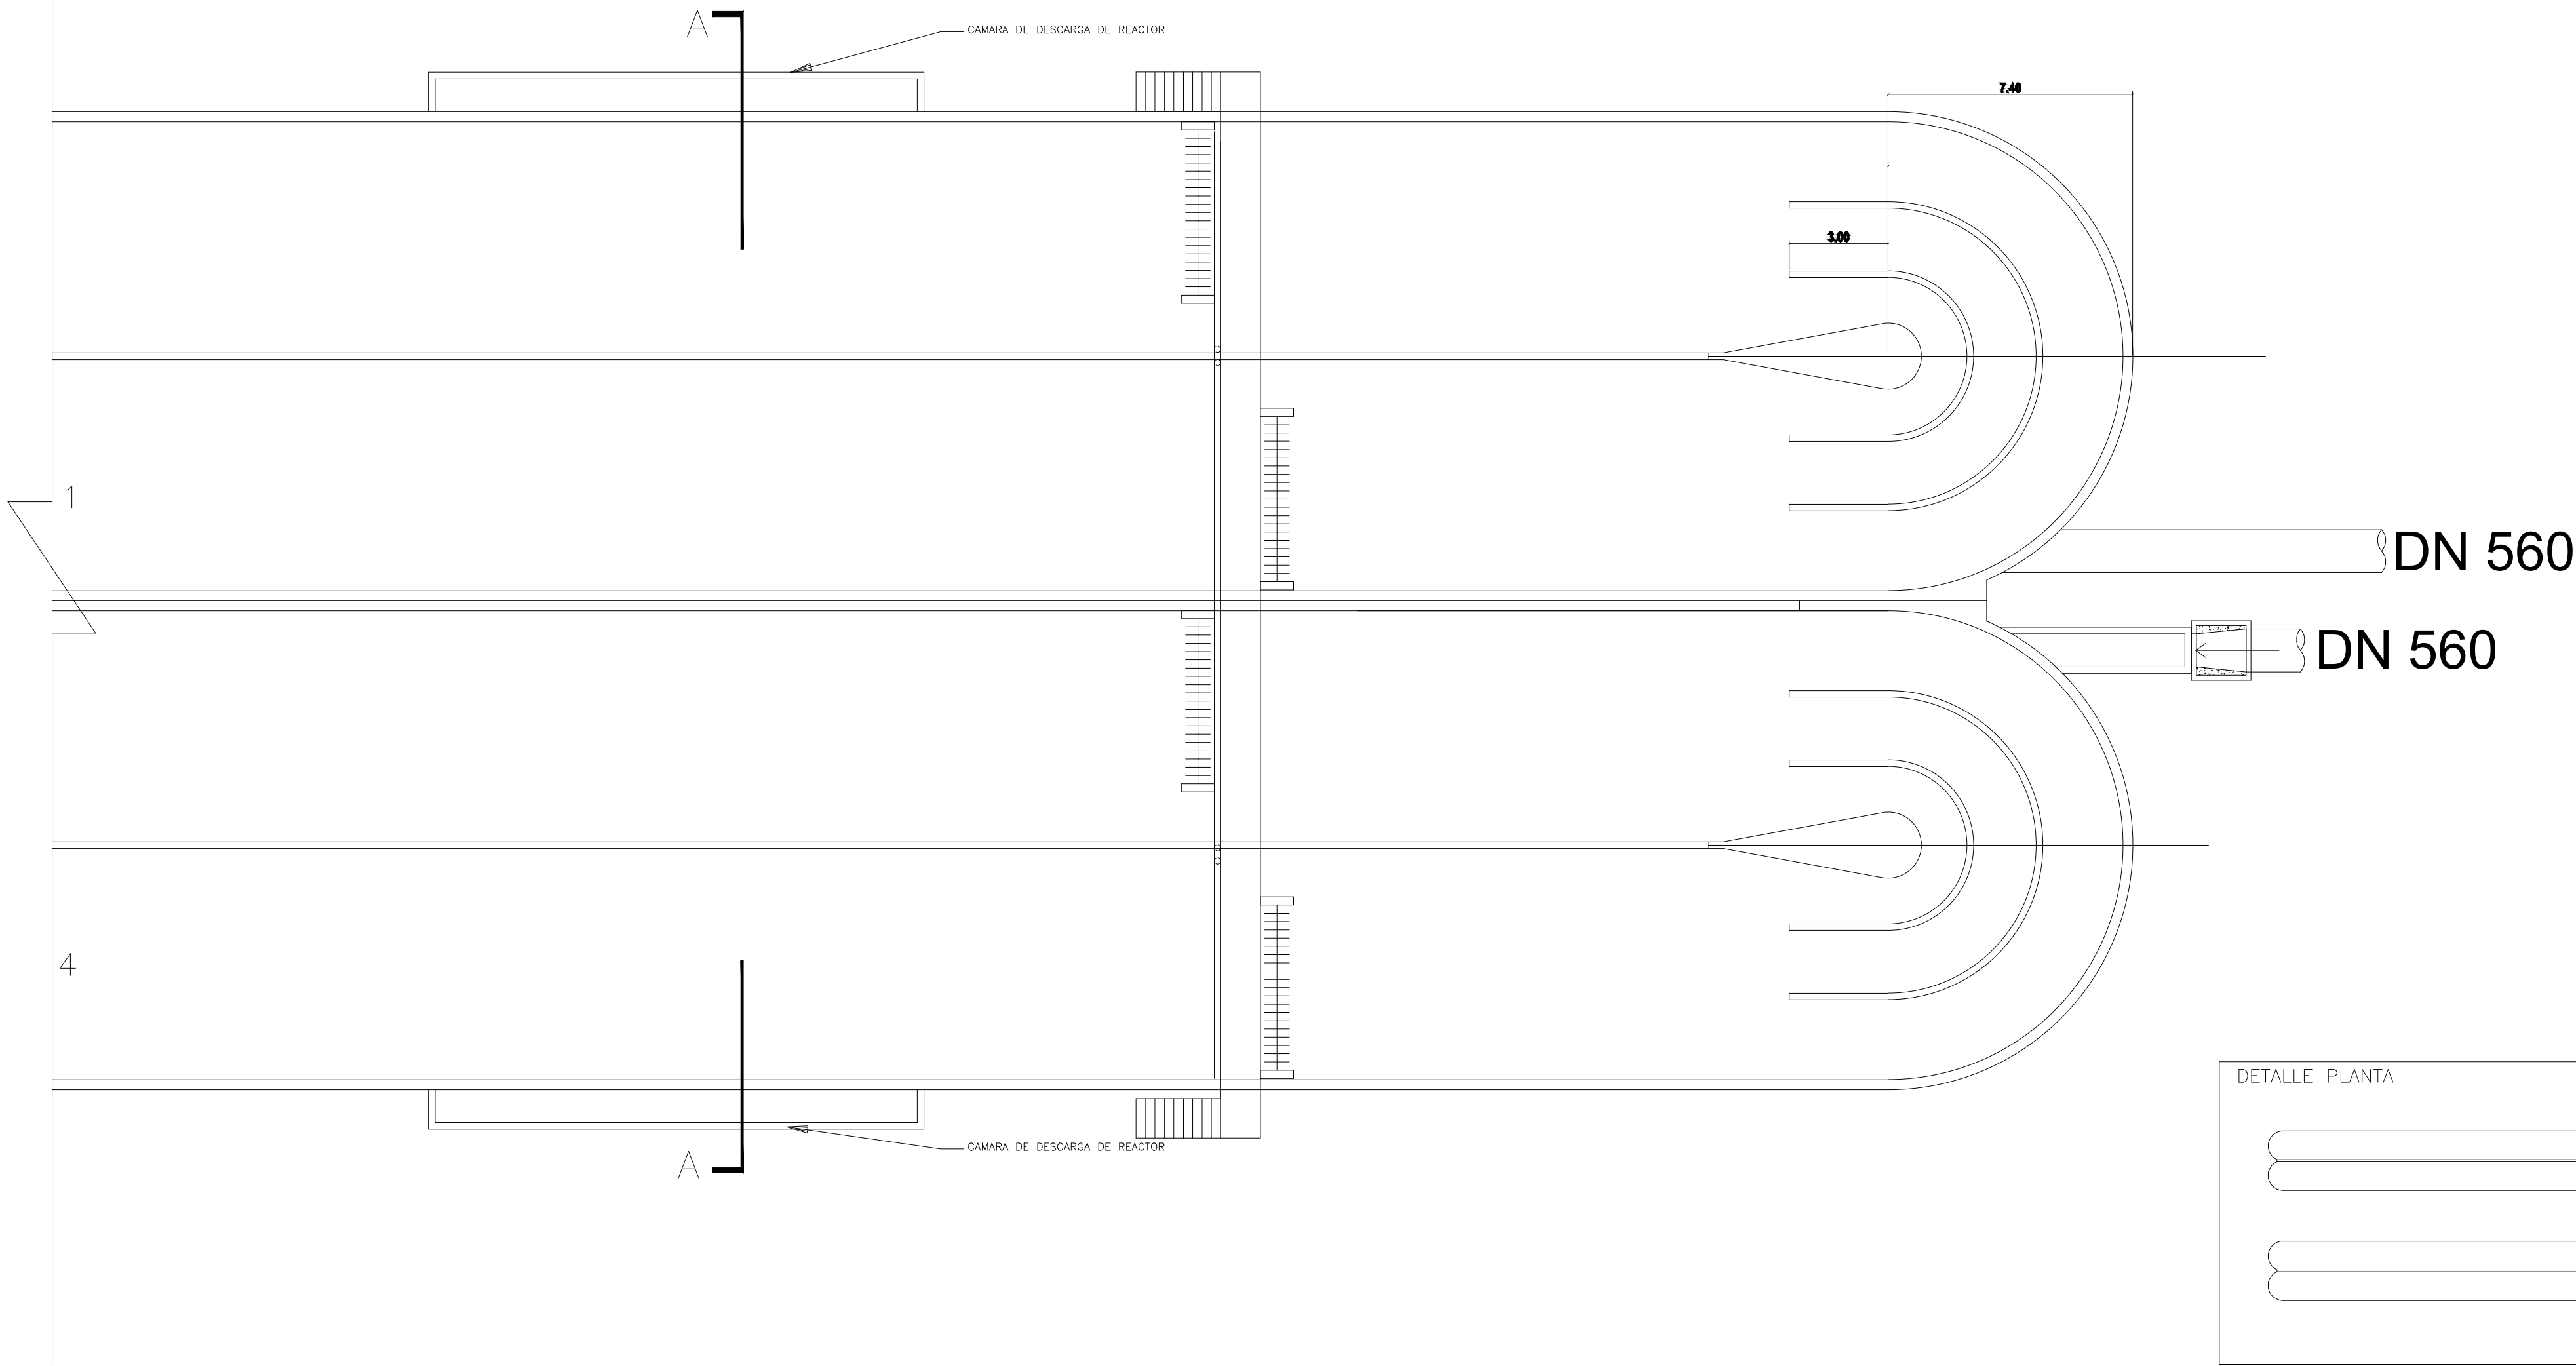


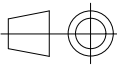
	FECHA	NOMBRE	PROYECTO FINAL	 FACULTAD REGIONAL SACTOENSE INSTITUTO TECNOLÓGICO NACIONAL
Dib.		Fernández, Juan I.		
Rev.				
Apr.			Visado	
ESCALA: INDICADA				
				
Taller: Rsp				
				Plano: REACTORES BIOLÓGICOS - PLANTA - CORTE
				Código: PL - 008

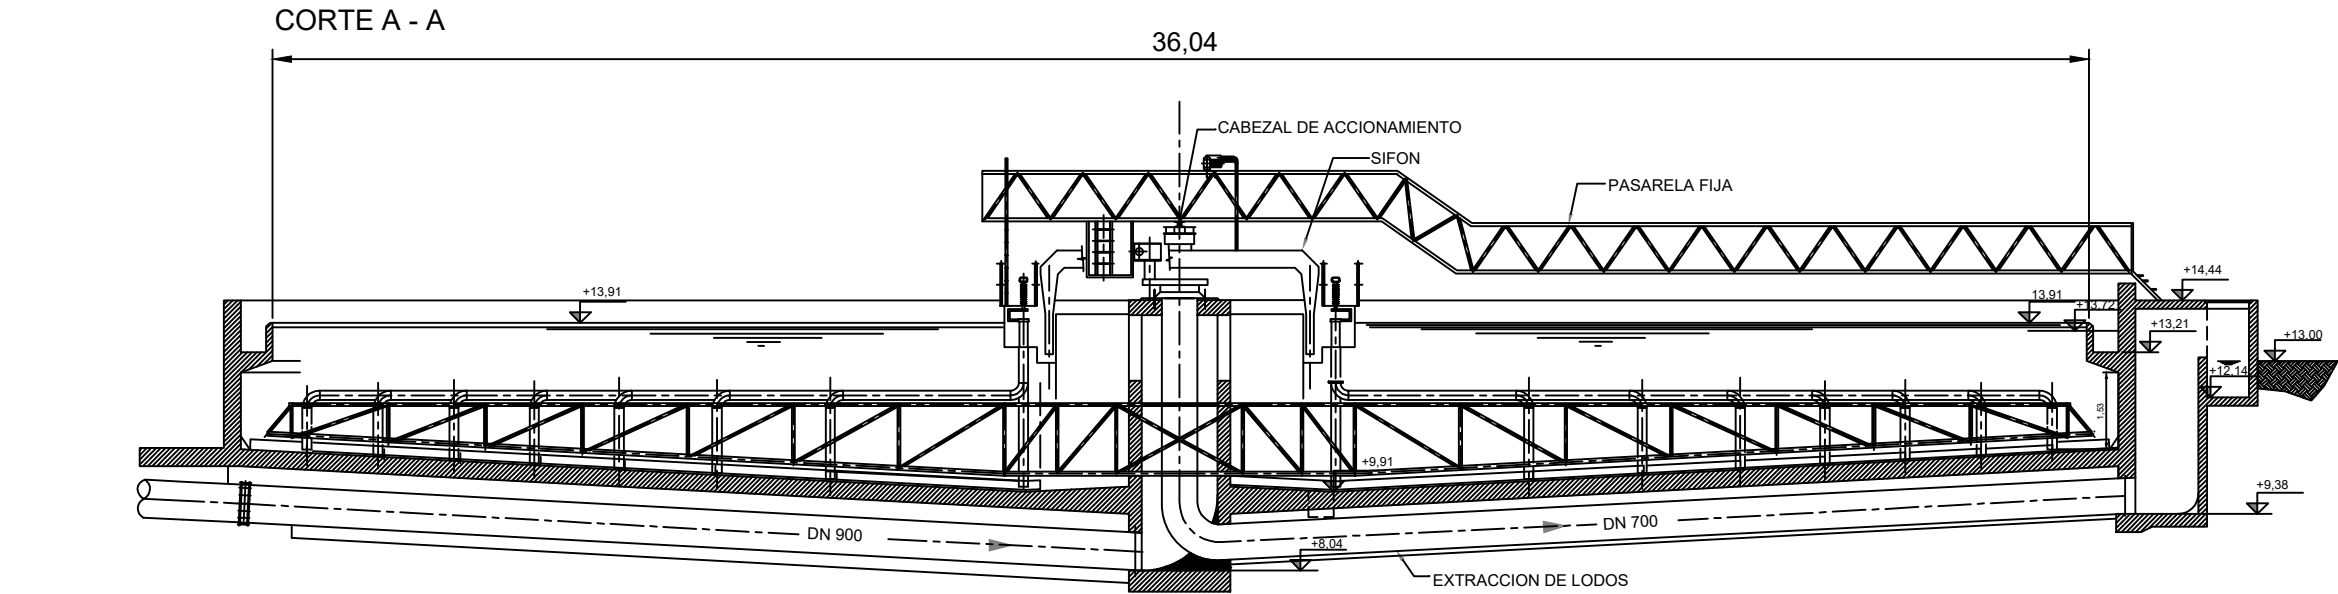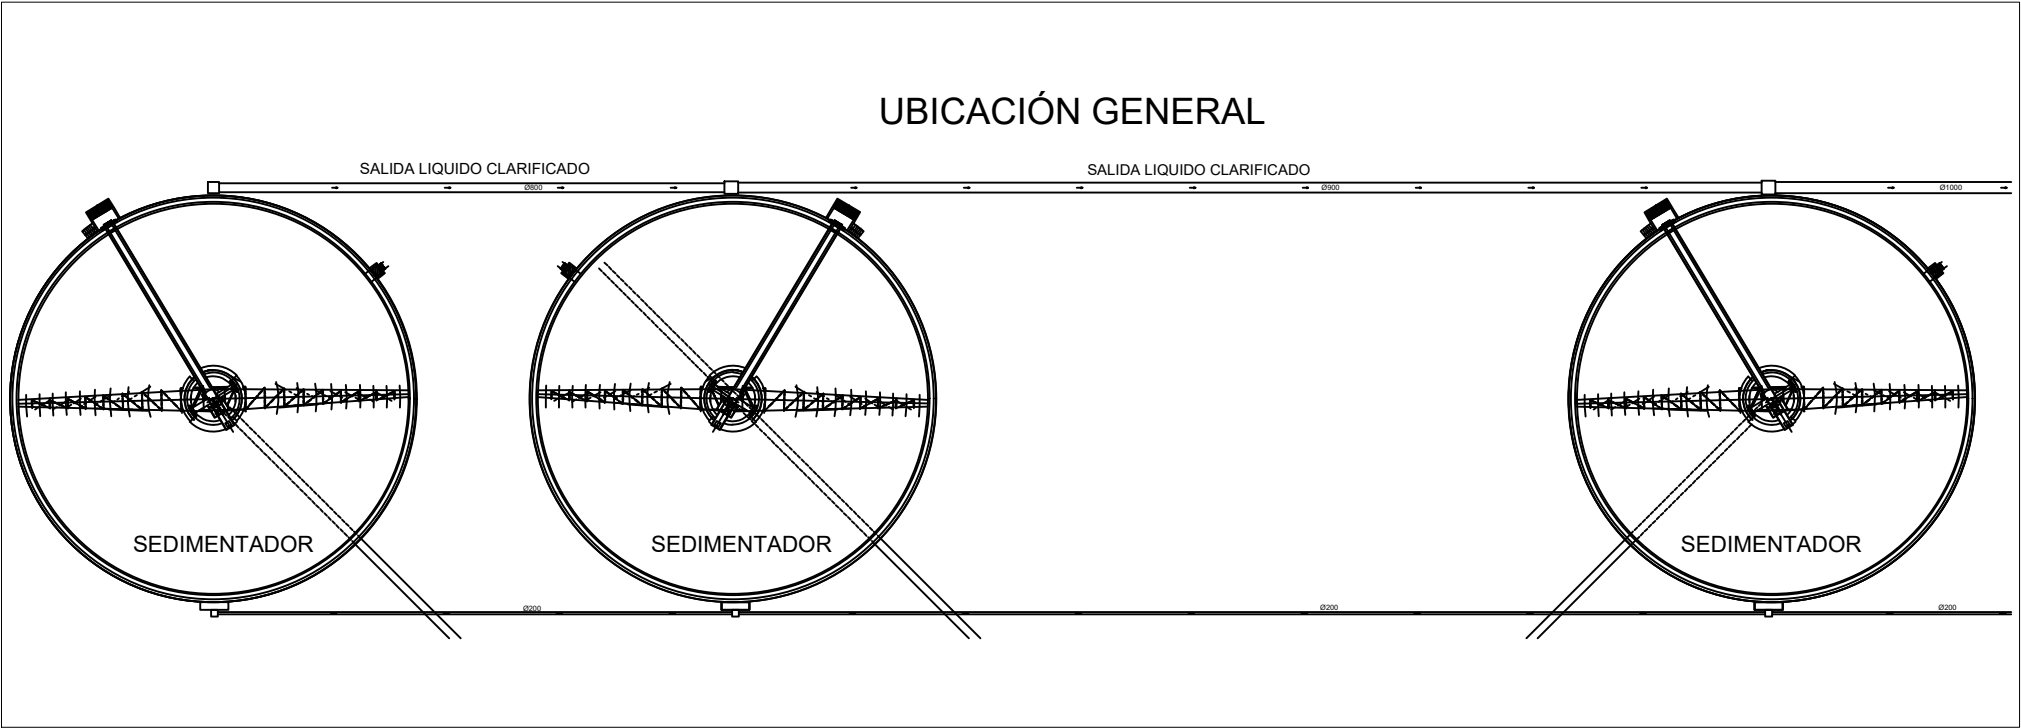
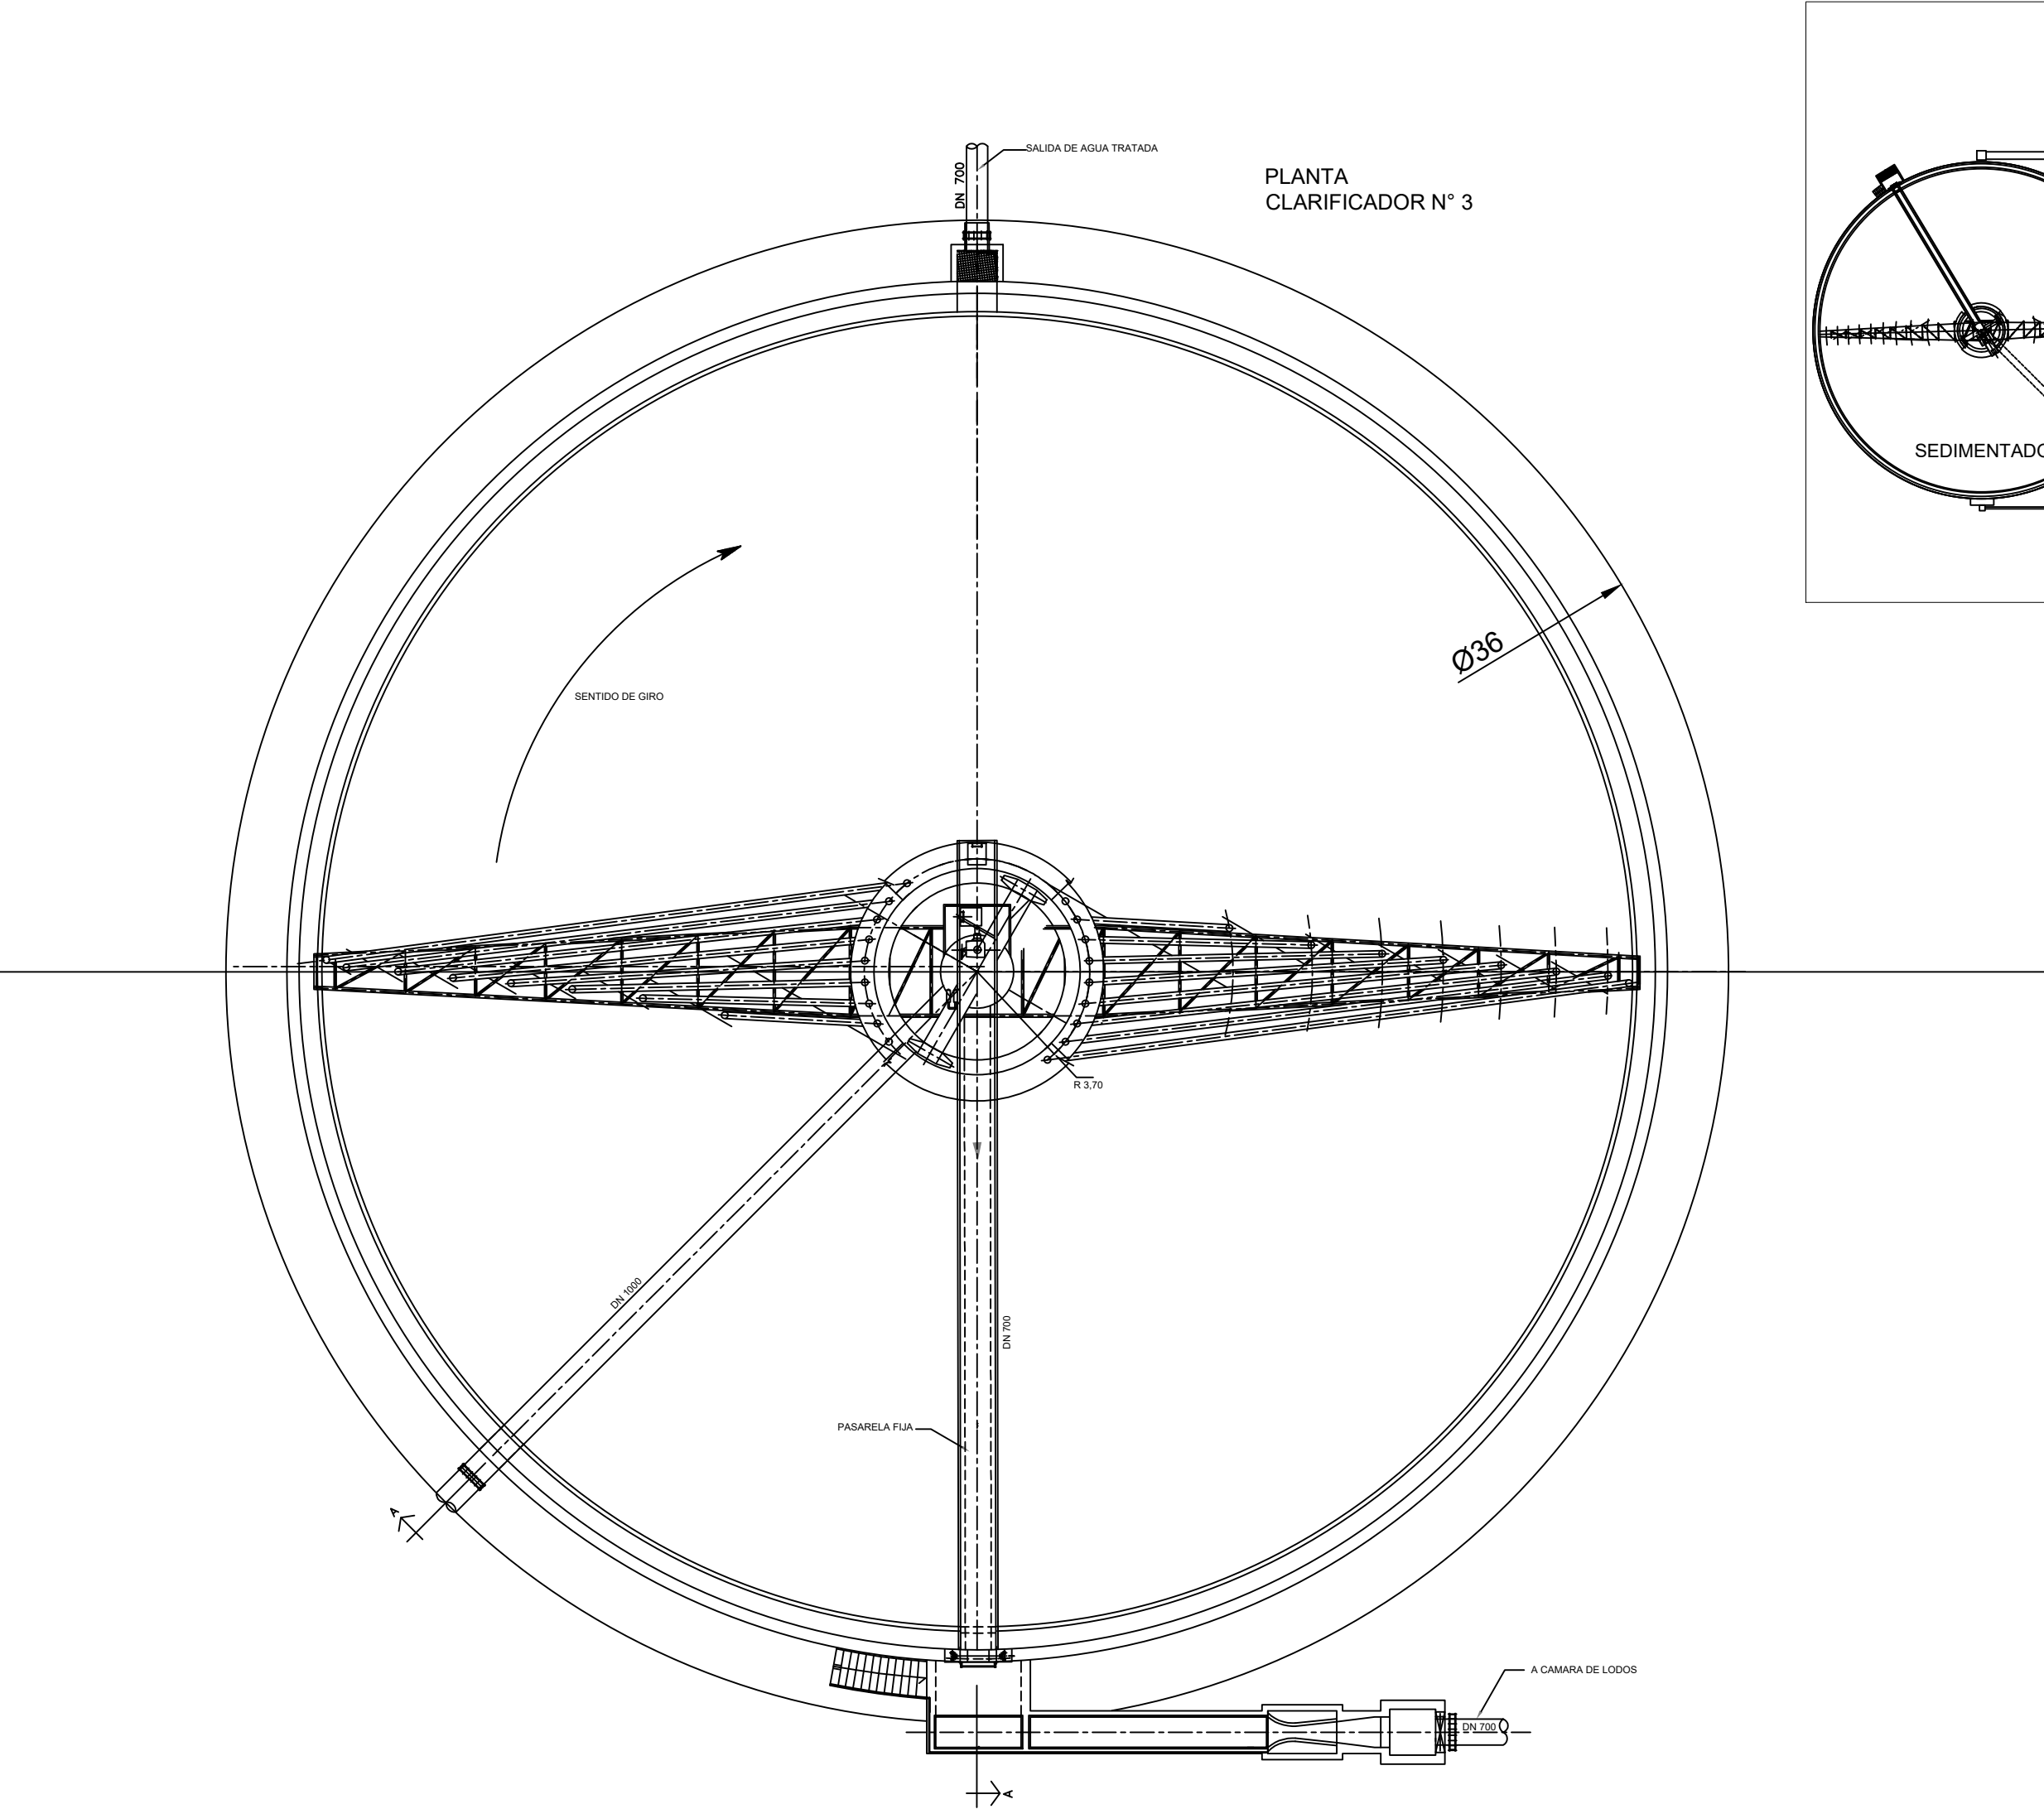


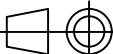
		FECHA	NOMBRE	PROYECTO FINAL	 FACULTAD REGIONAL SANTA CRUZ UNIVERSIDAD TECNOLÓGICA NACIONAL
Dib.		Fernández, Juan I.			
Rev.					
Apr.					
ESCALA: 1:150					Visado
					
Toler. Rug.					
					Plano: CLARIFICADOR
					Código: PL - 009


ESPESADOR - PLANTA

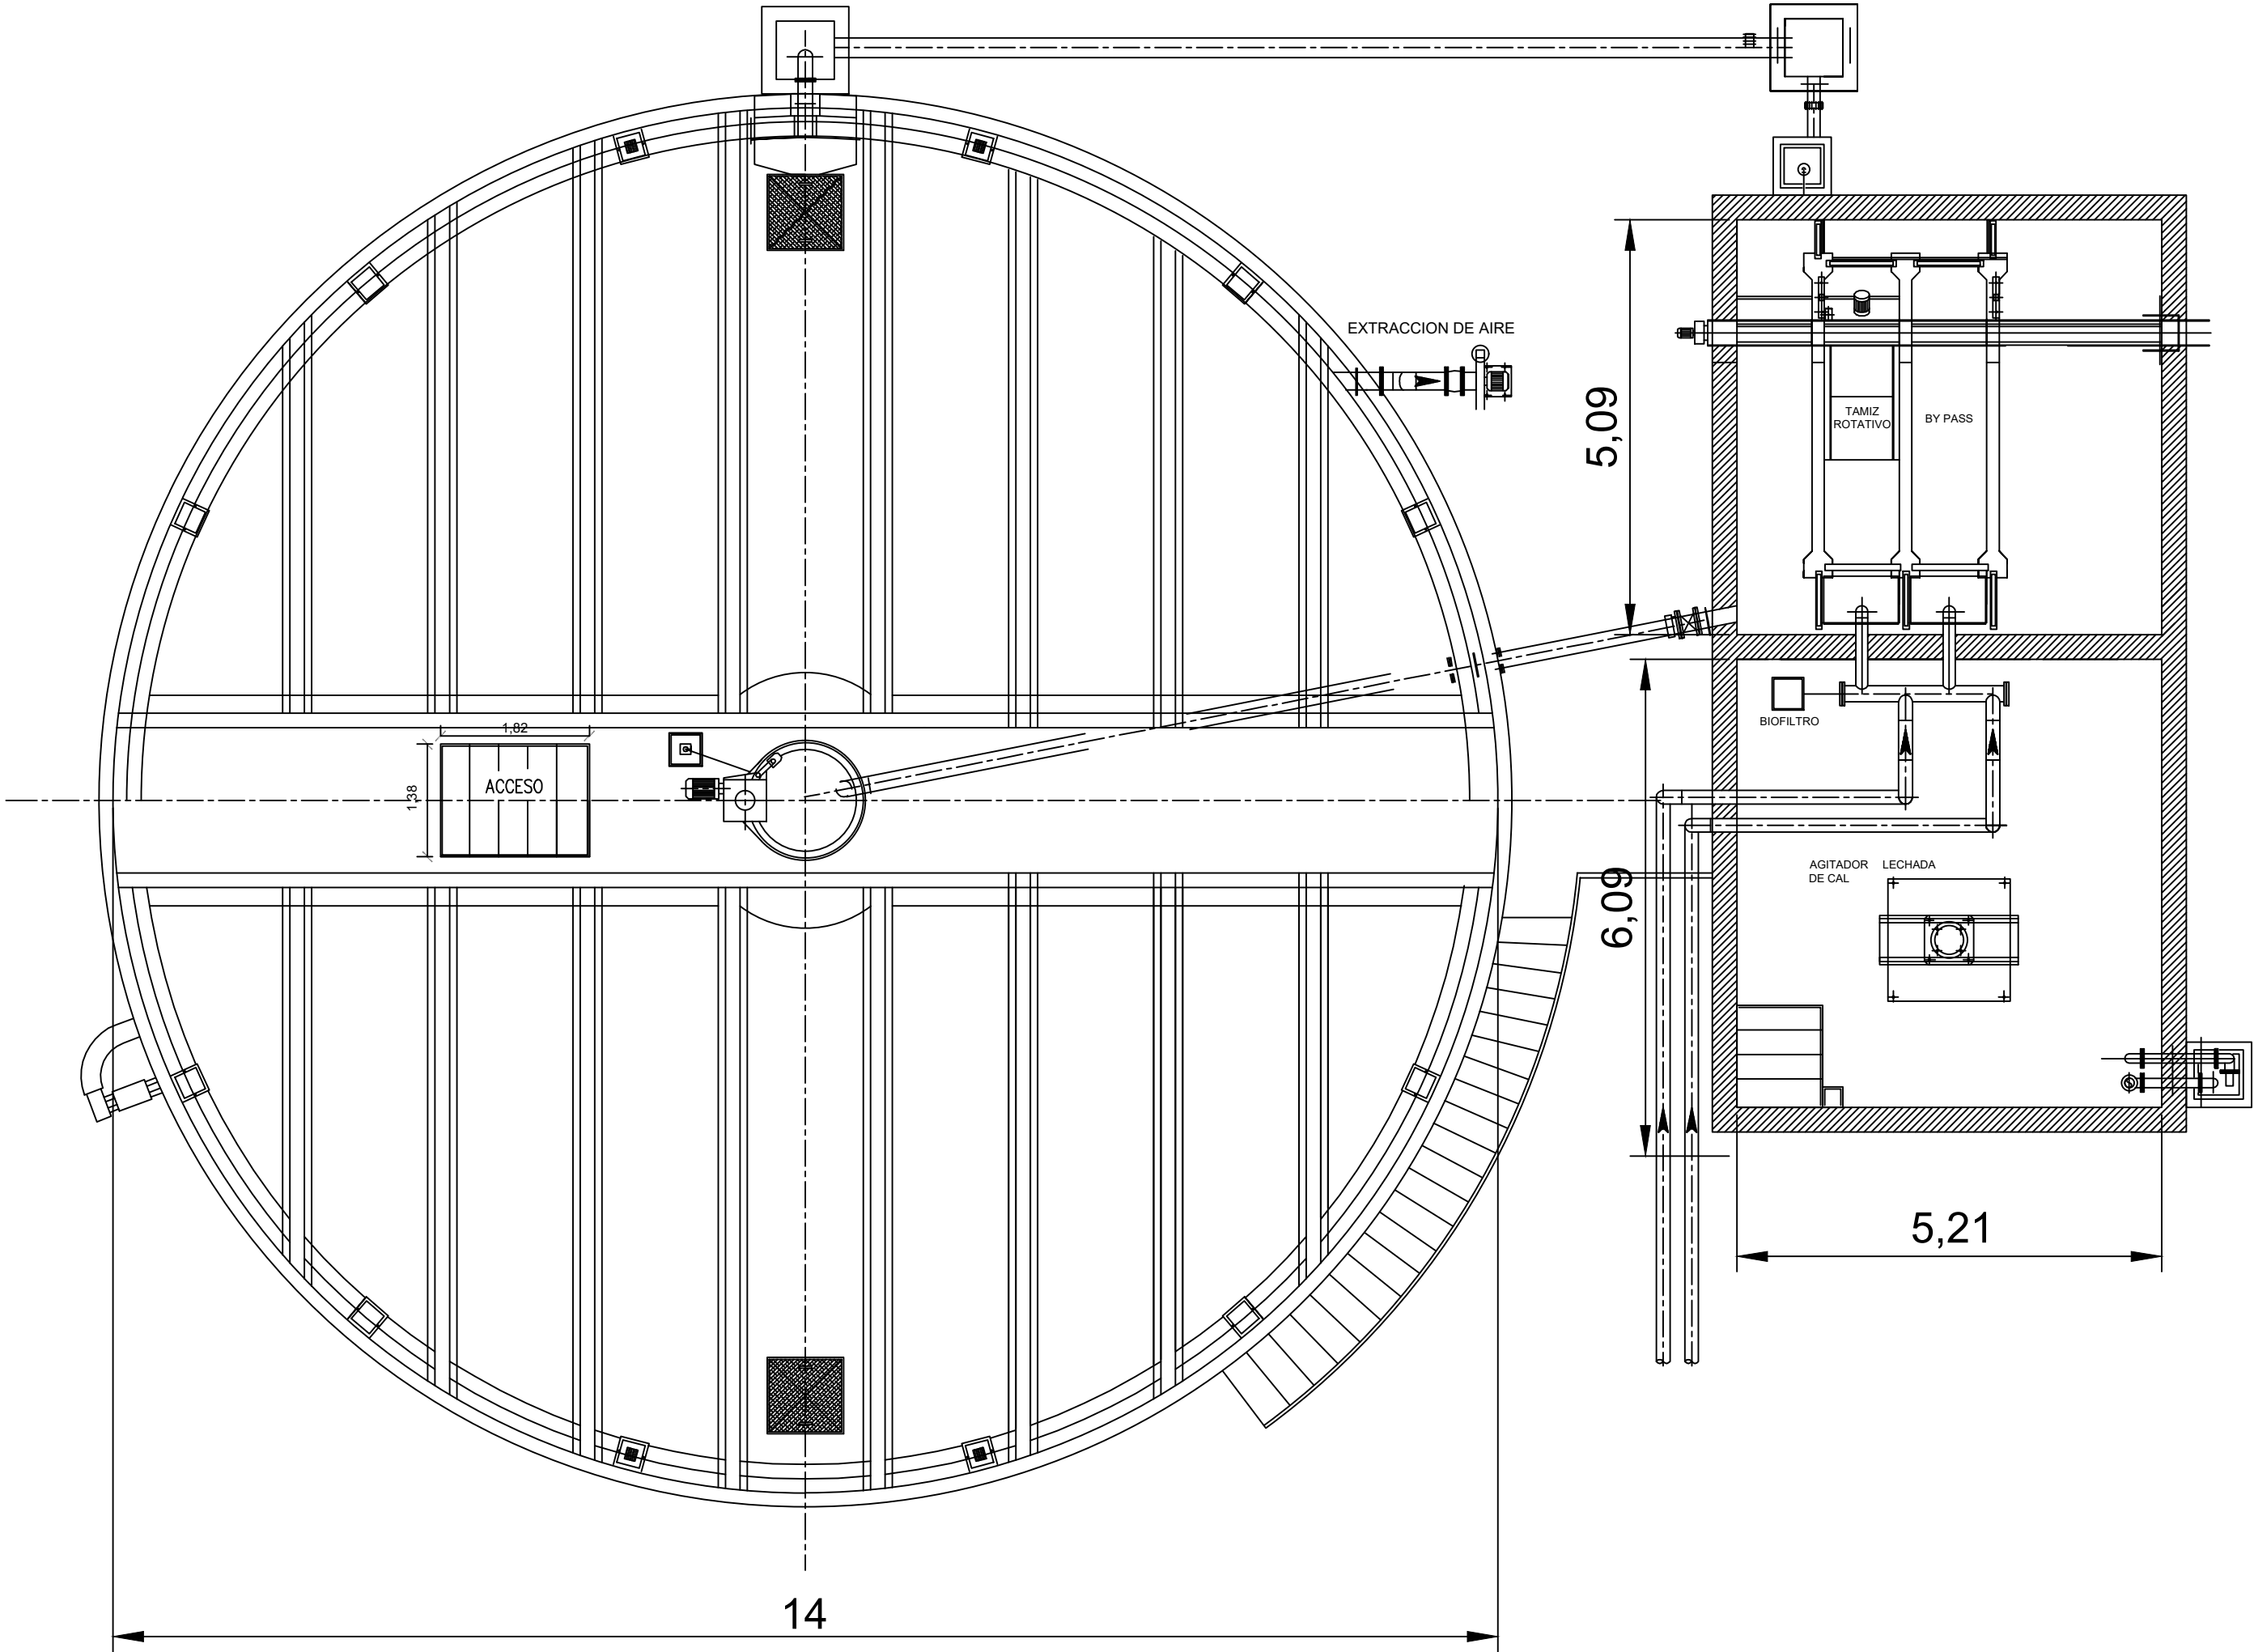

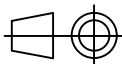
		FECHA	NOMBRE	PROYECTO FINAL	 FACULTAD REGIONAL SANTA CRUZ UNIVERSIDAD TECNOLÓGICA NACIONAL
Dib.		Fernández, Juan I.			
Rev.					
Apr.					
ESCALA: 1:75					Visado
					
Toler. Rug.					
					Plano: ESPESADOR DE LODOS - PLANTA
					Código: PL - 010

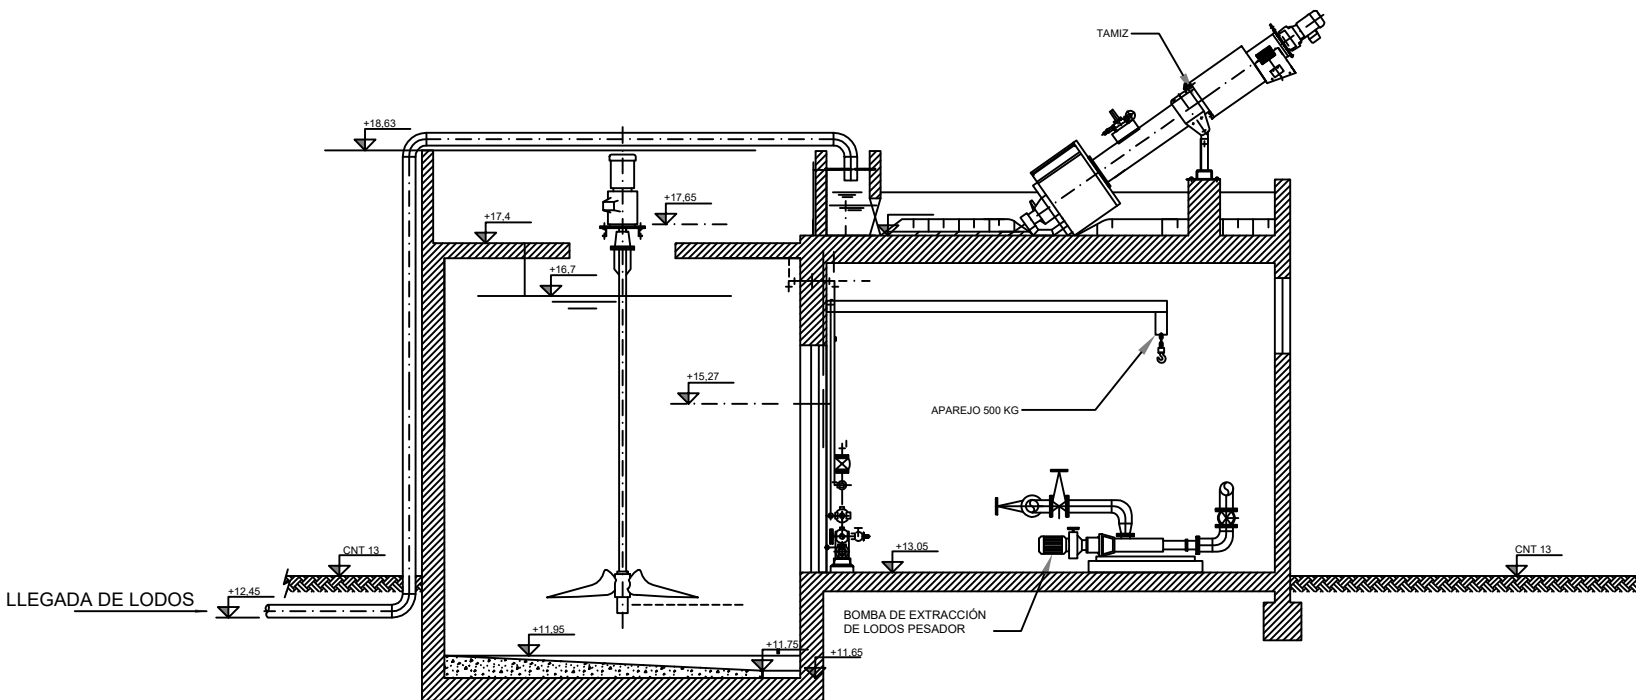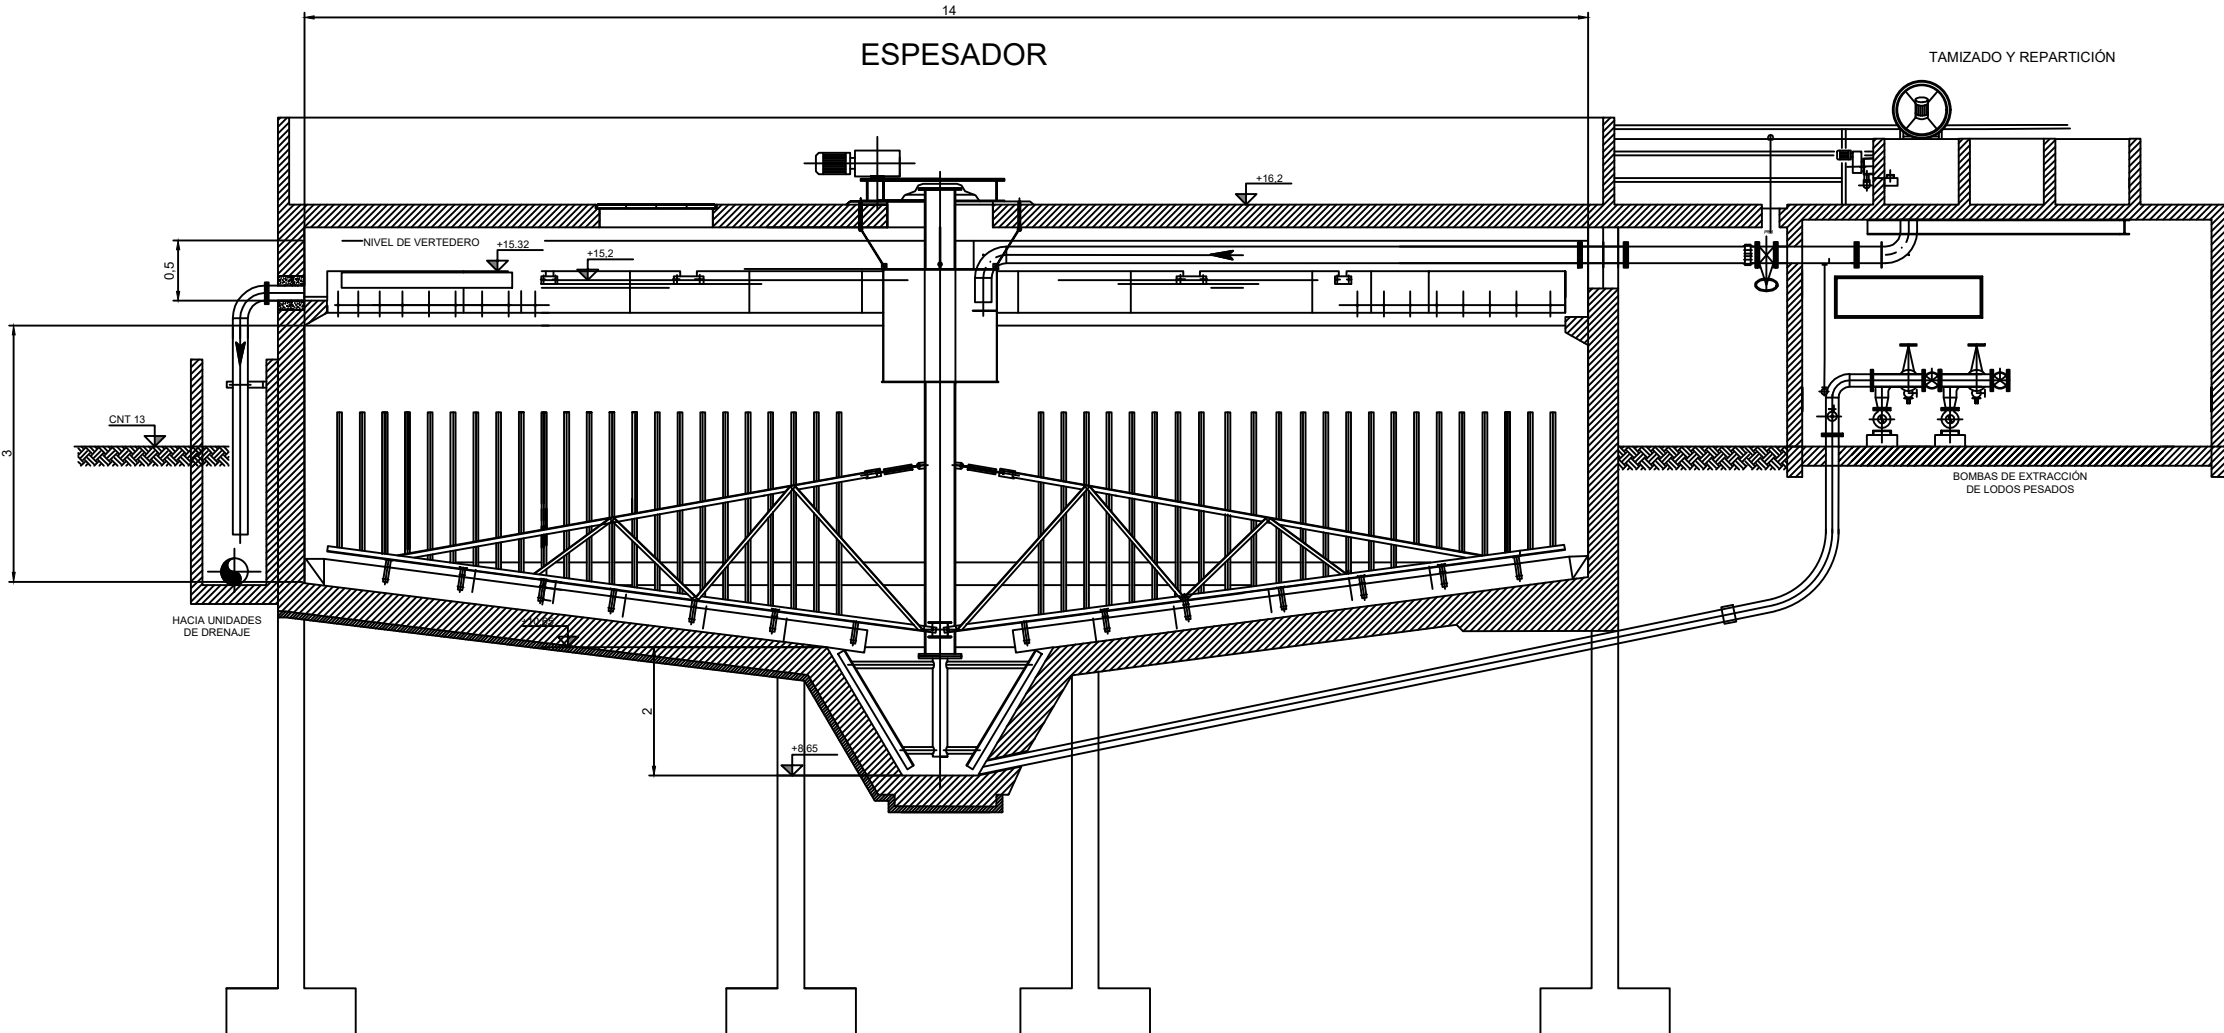


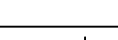		FECHA	NOMBRE	PROYECTO FINAL	 UTN FACULTAD REGIONAL SANTA CRUZ UNIVERSIDAD TECNOLÓGICA NACIONAL
Dib.			Fernández, Juan I.		
Rev.					
Apr.					
ESCALA: 1:100					Visado
					Piano: ESPESADOR DE LODOS - CORTES
Toler. Rug.					Código: PL - 011

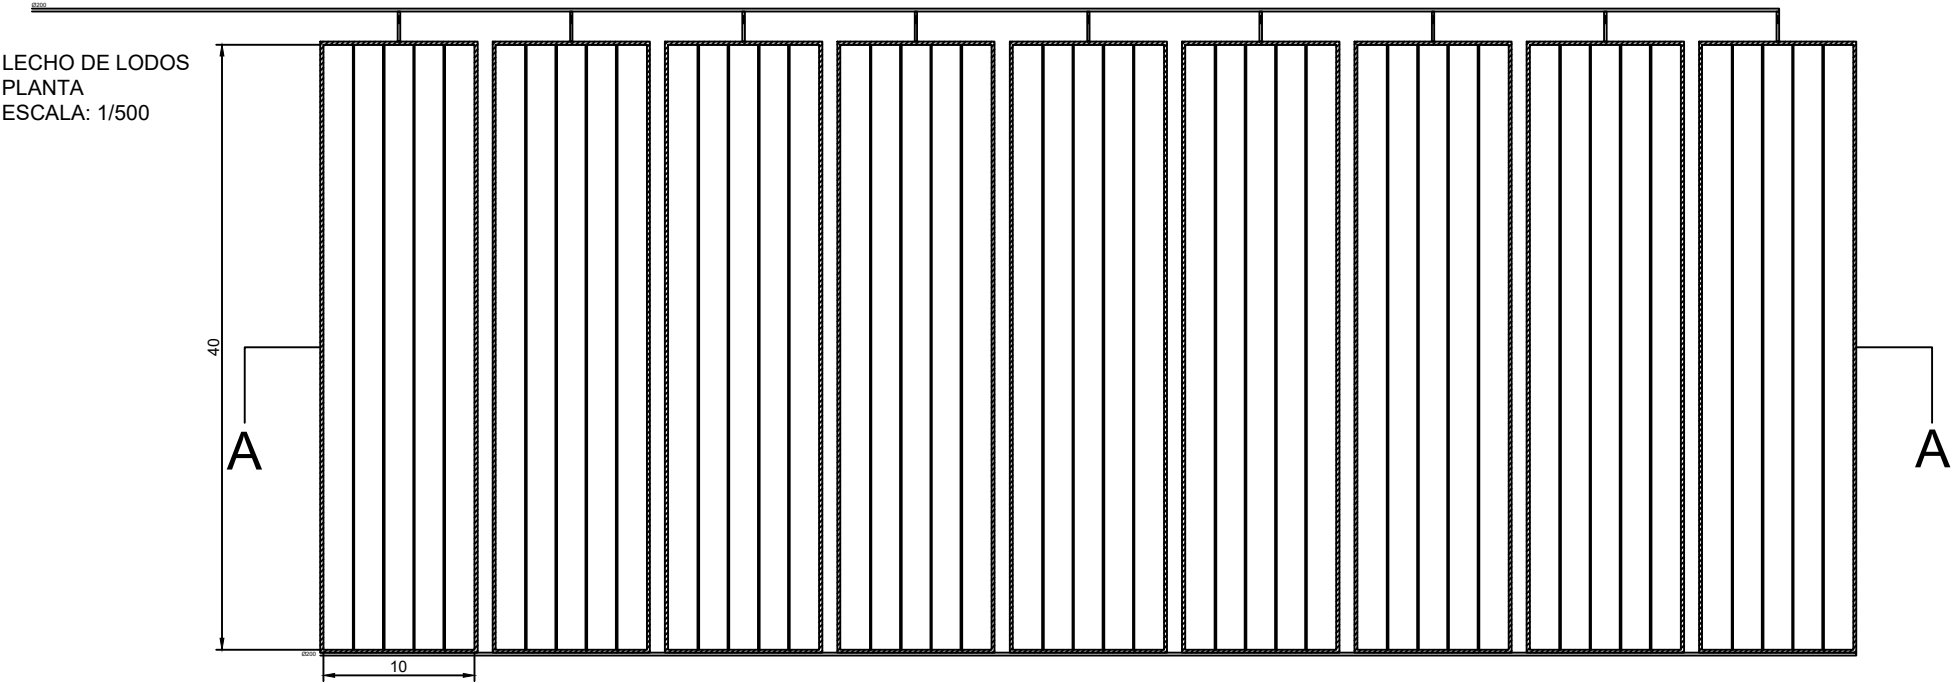


LECHO DE LODOS
CORTE A - A
ESCALA: 1/30

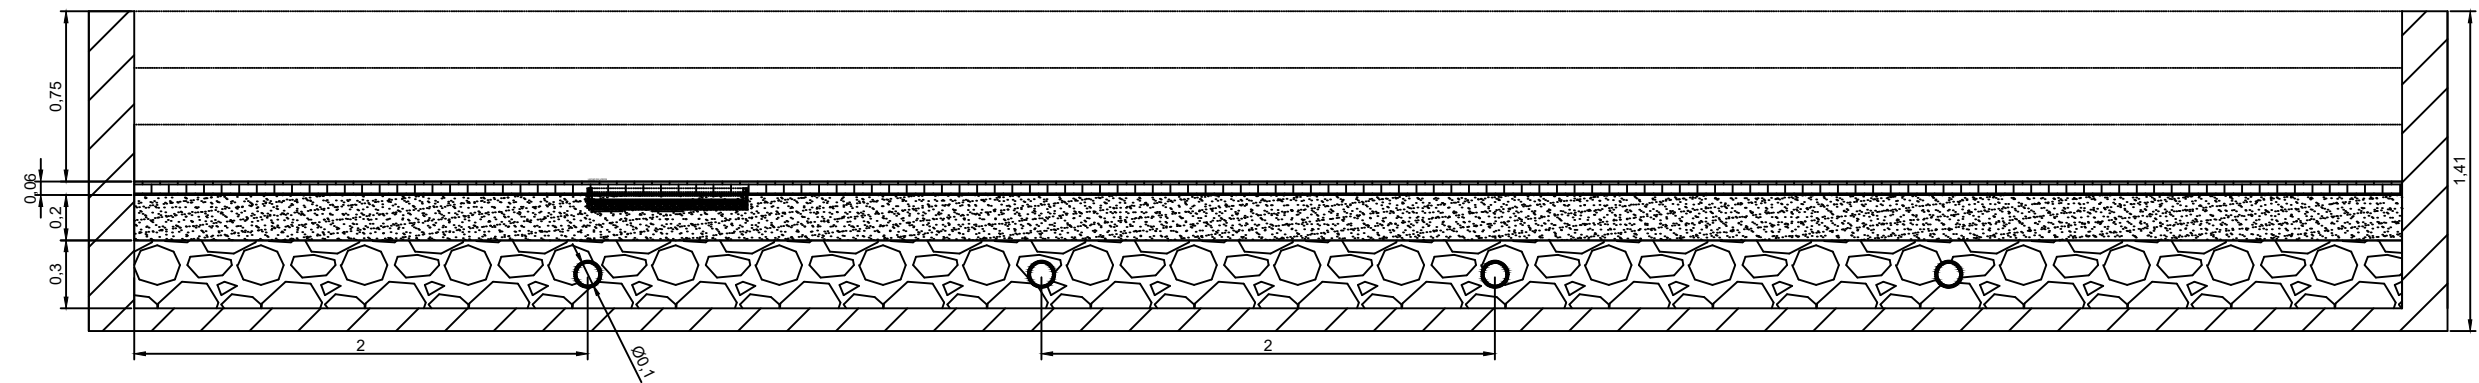


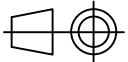
		FECHA	NOMBRE	PROYECTO FINAL	 FACULTAD REGIONAL SANTA CRUZ UNIVERSIDAD TECNOLÓGICA NACIONAL
	Dib.		Fernández, Juan I.		
	Rev.				
	Apr.				
	ESCALA: INDICADA				Visado
	Plano: LECHOS DE SECADO - PLANTA - CORTE				
Toler. Rug.	Código: PL - 012				

PLANTA
ESCALA:1:250

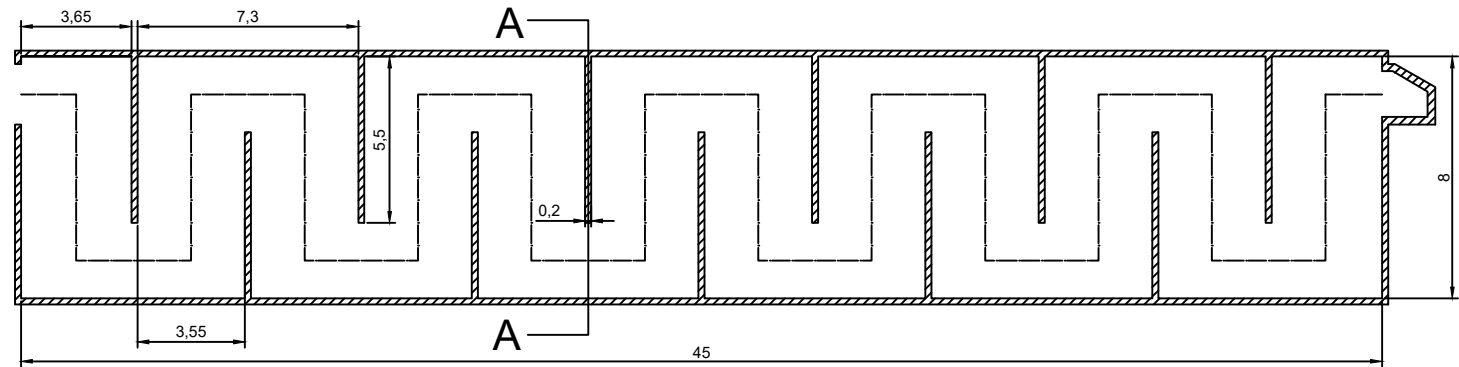

CORTE A - A
ESCALA:1:75

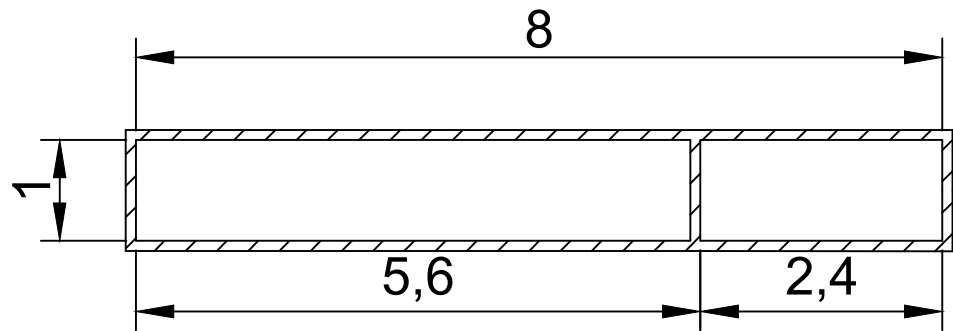

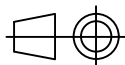		FECHA	NOMBRE	PROYECTO FINAL	
	Dib.		Fernández, Juan I.		
	Rev.				
	Apr.				
	ESCALA: INDICADA				Visado
					
	Toler. Rug.				
					Plano: CÁMARA DE CONTACTO
					Código: PL - 013